

Phones	Fax
+357 99 882907	+357 24 650846
+357 99 640508	

**Address**  
Nikodimou Milona 28,  
Sunorama House, off. 401,  
6050 Larnaka

**Email:**  
[info@cgpchristou.com](mailto:info@cgpchristou.com)

**Description**

**Client Name**  
PAPANTONIS NIKOLAIDIS

**City/Village**  
LIMASSOL / ZAKAKI

**Sheet Name**  
GROUND FLOOR PLAN


**Project number**

**Date** 09/23

**Sheet number**


A1

**Scale** 1:100

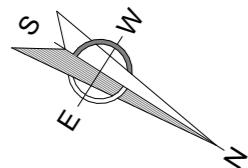

## GROUND FLOOR PLAN

1 : 100

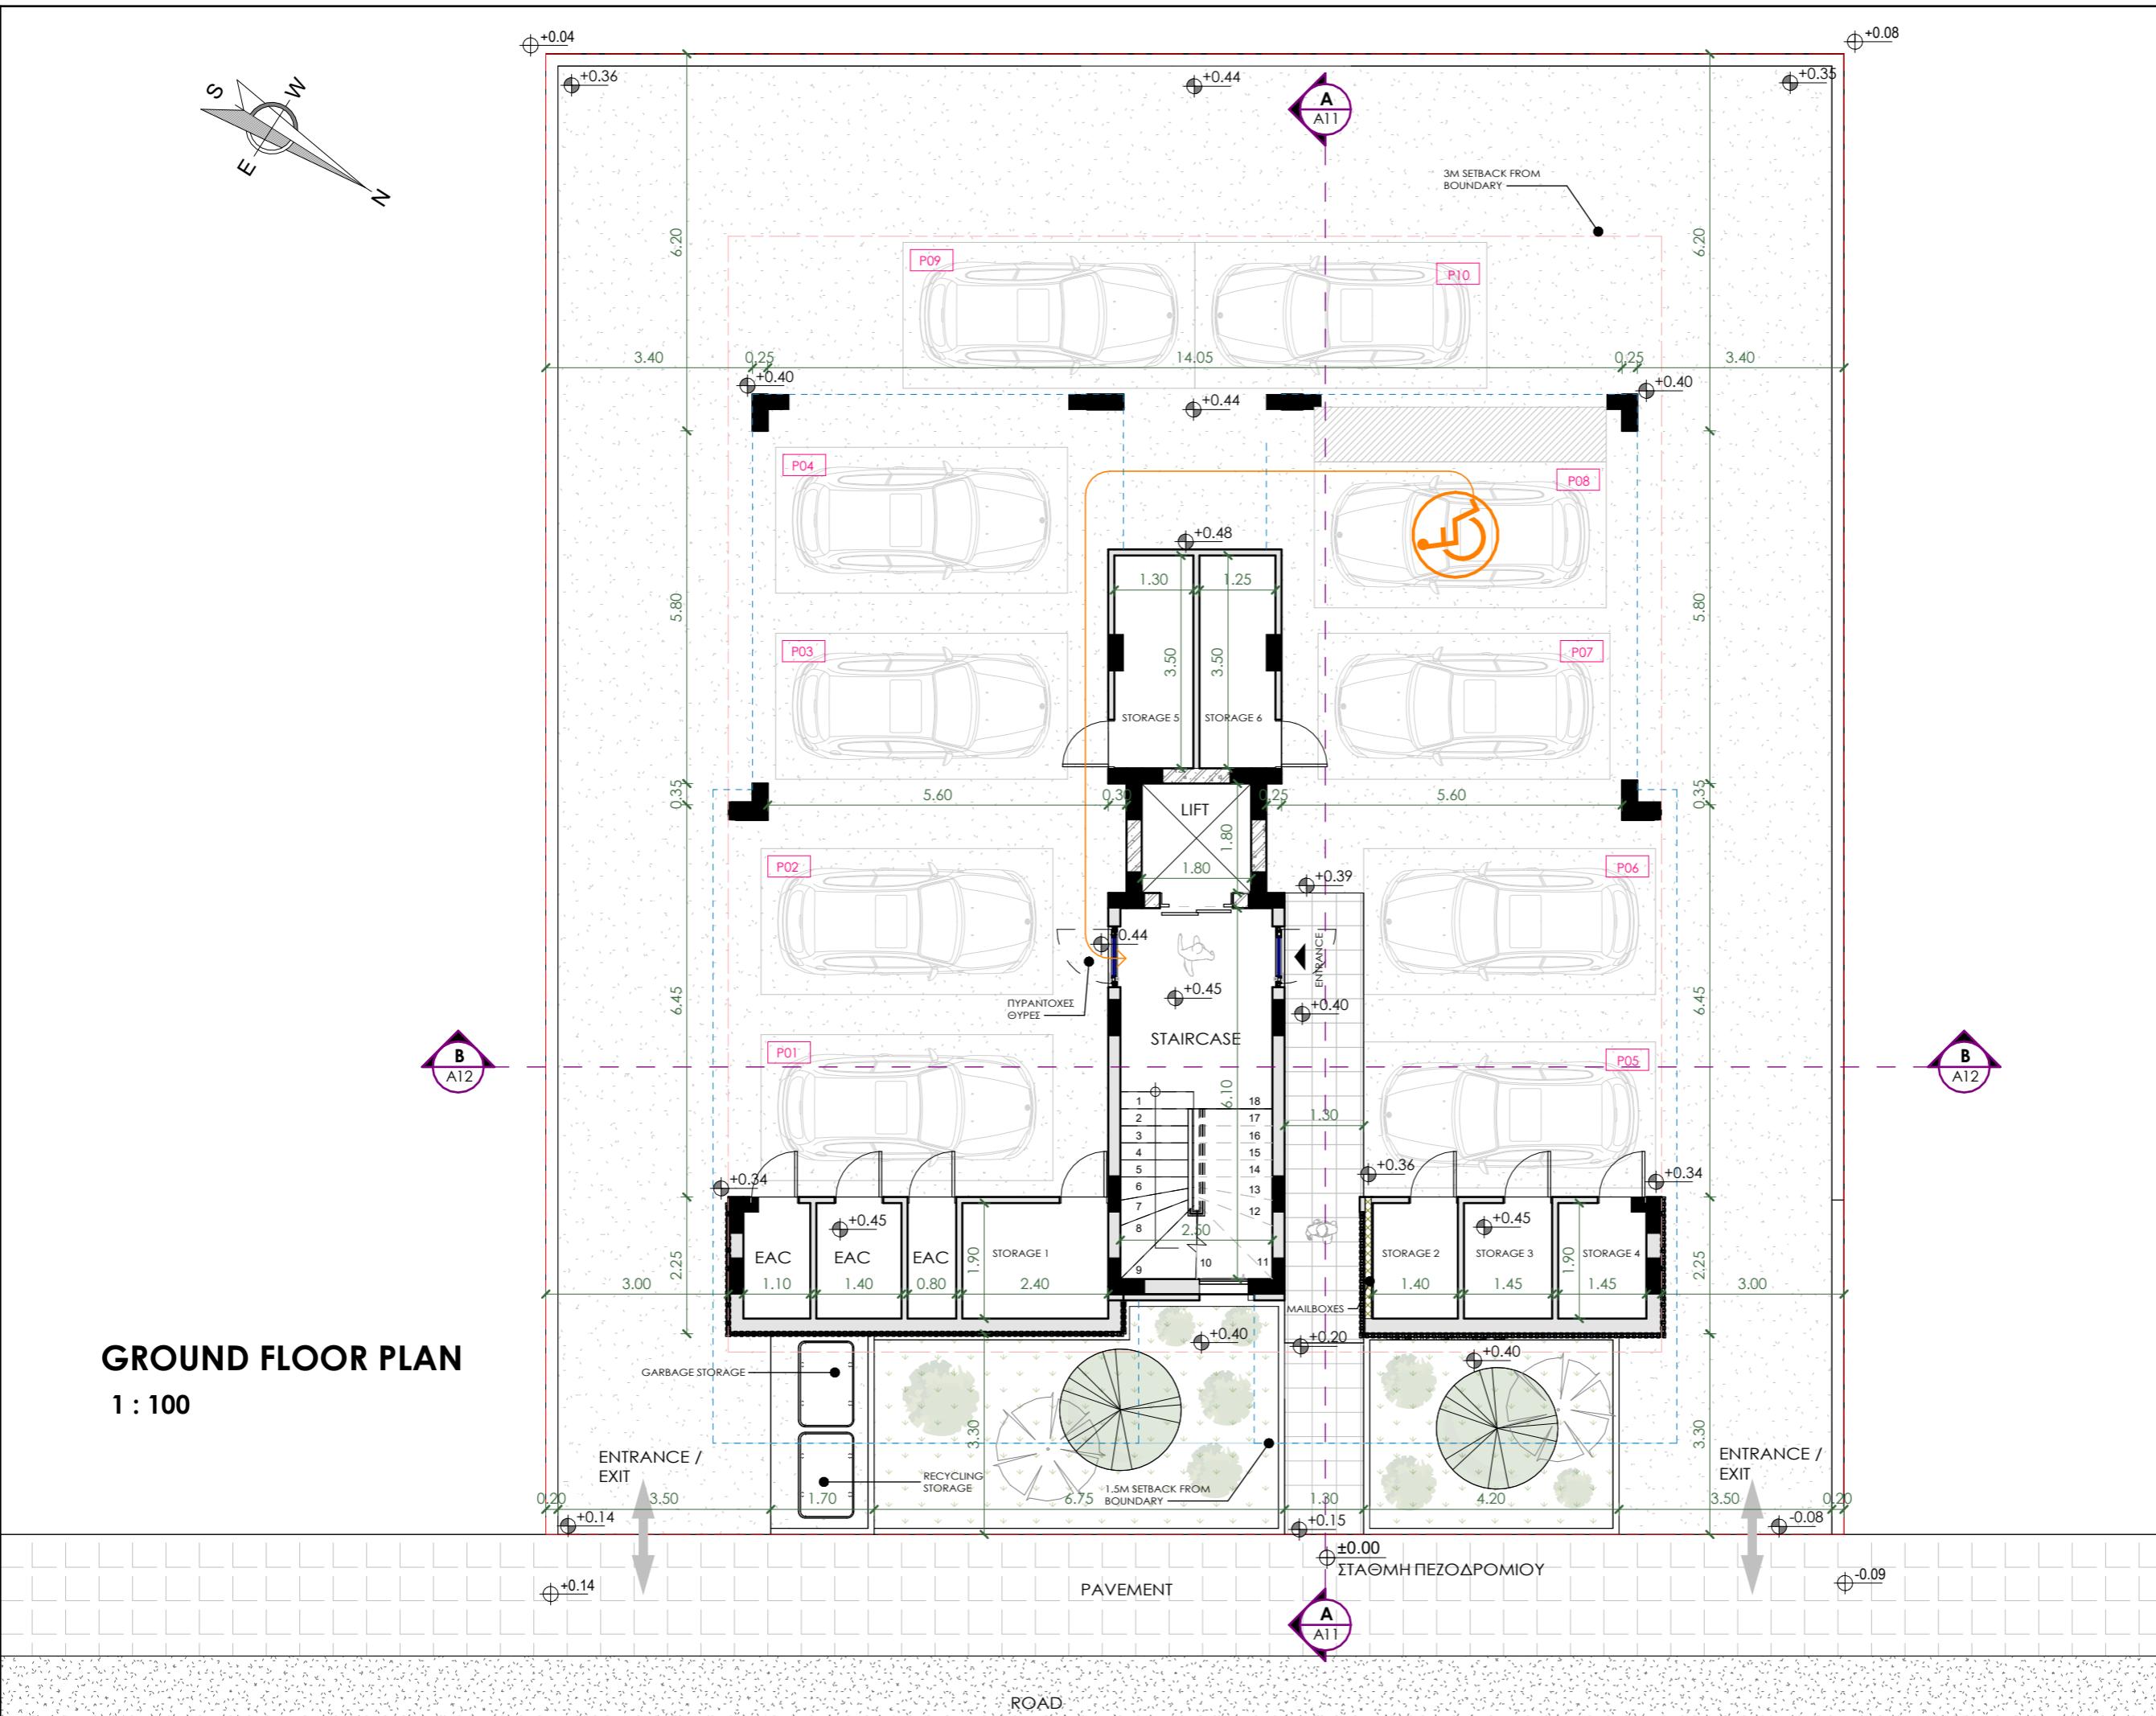



Phones +357 99 882907  
Fax +357 24 650846  
+357 99 640508

Address  
Nikodimou Milona 28,  
Sunorama House, off. 401,  
6050 Larnaka

Email:  
info@cgchristou.com

Description

Client Name  
PAPANTONIS NIKOLAIDIS

City/Village  
LIMASSOL / ZAKAKI



Sheet Name  
FIRST FLOOR PLAN

Project number  
09/23

Date  
09/23

Sheet number  
A2

Scale  
1 : 100

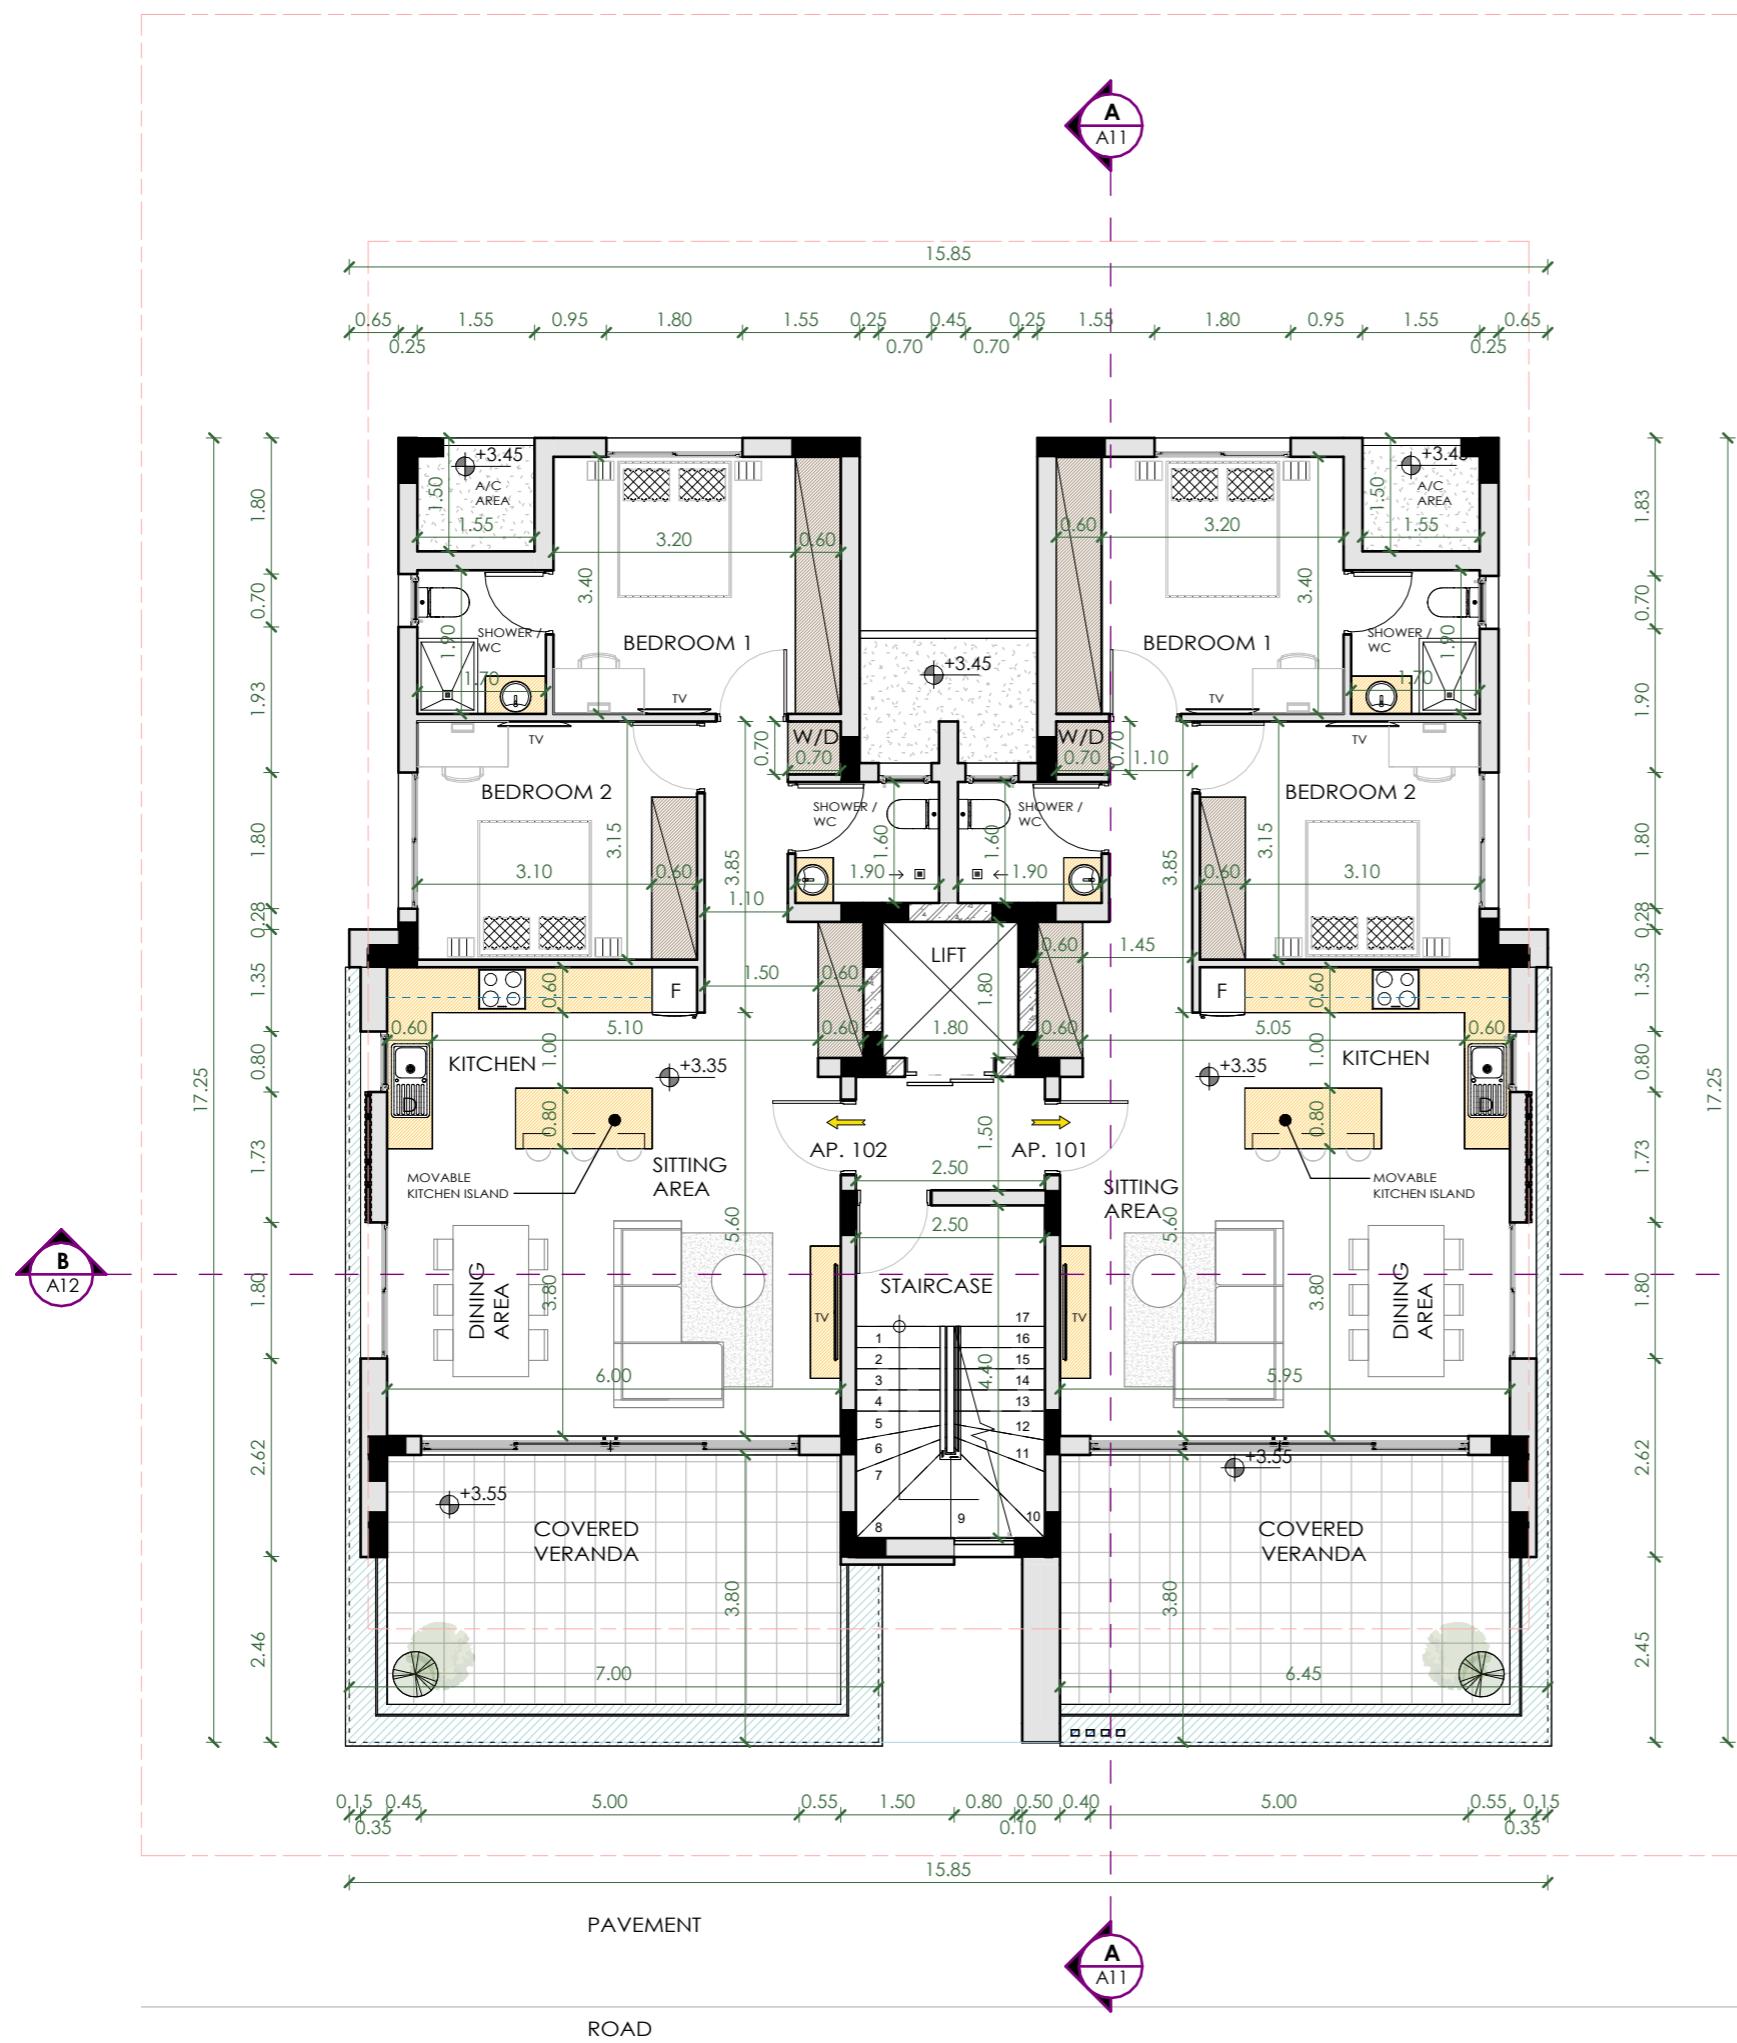
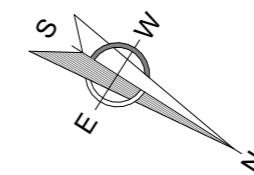


## FIRST FLOOR PLAN

1 : 100



NOTES:

- F = FRIDGE
- AP = APARTMENT
- W/D = WASHING MACHINE/DRYER MACHINE
- D = DISH WASHER

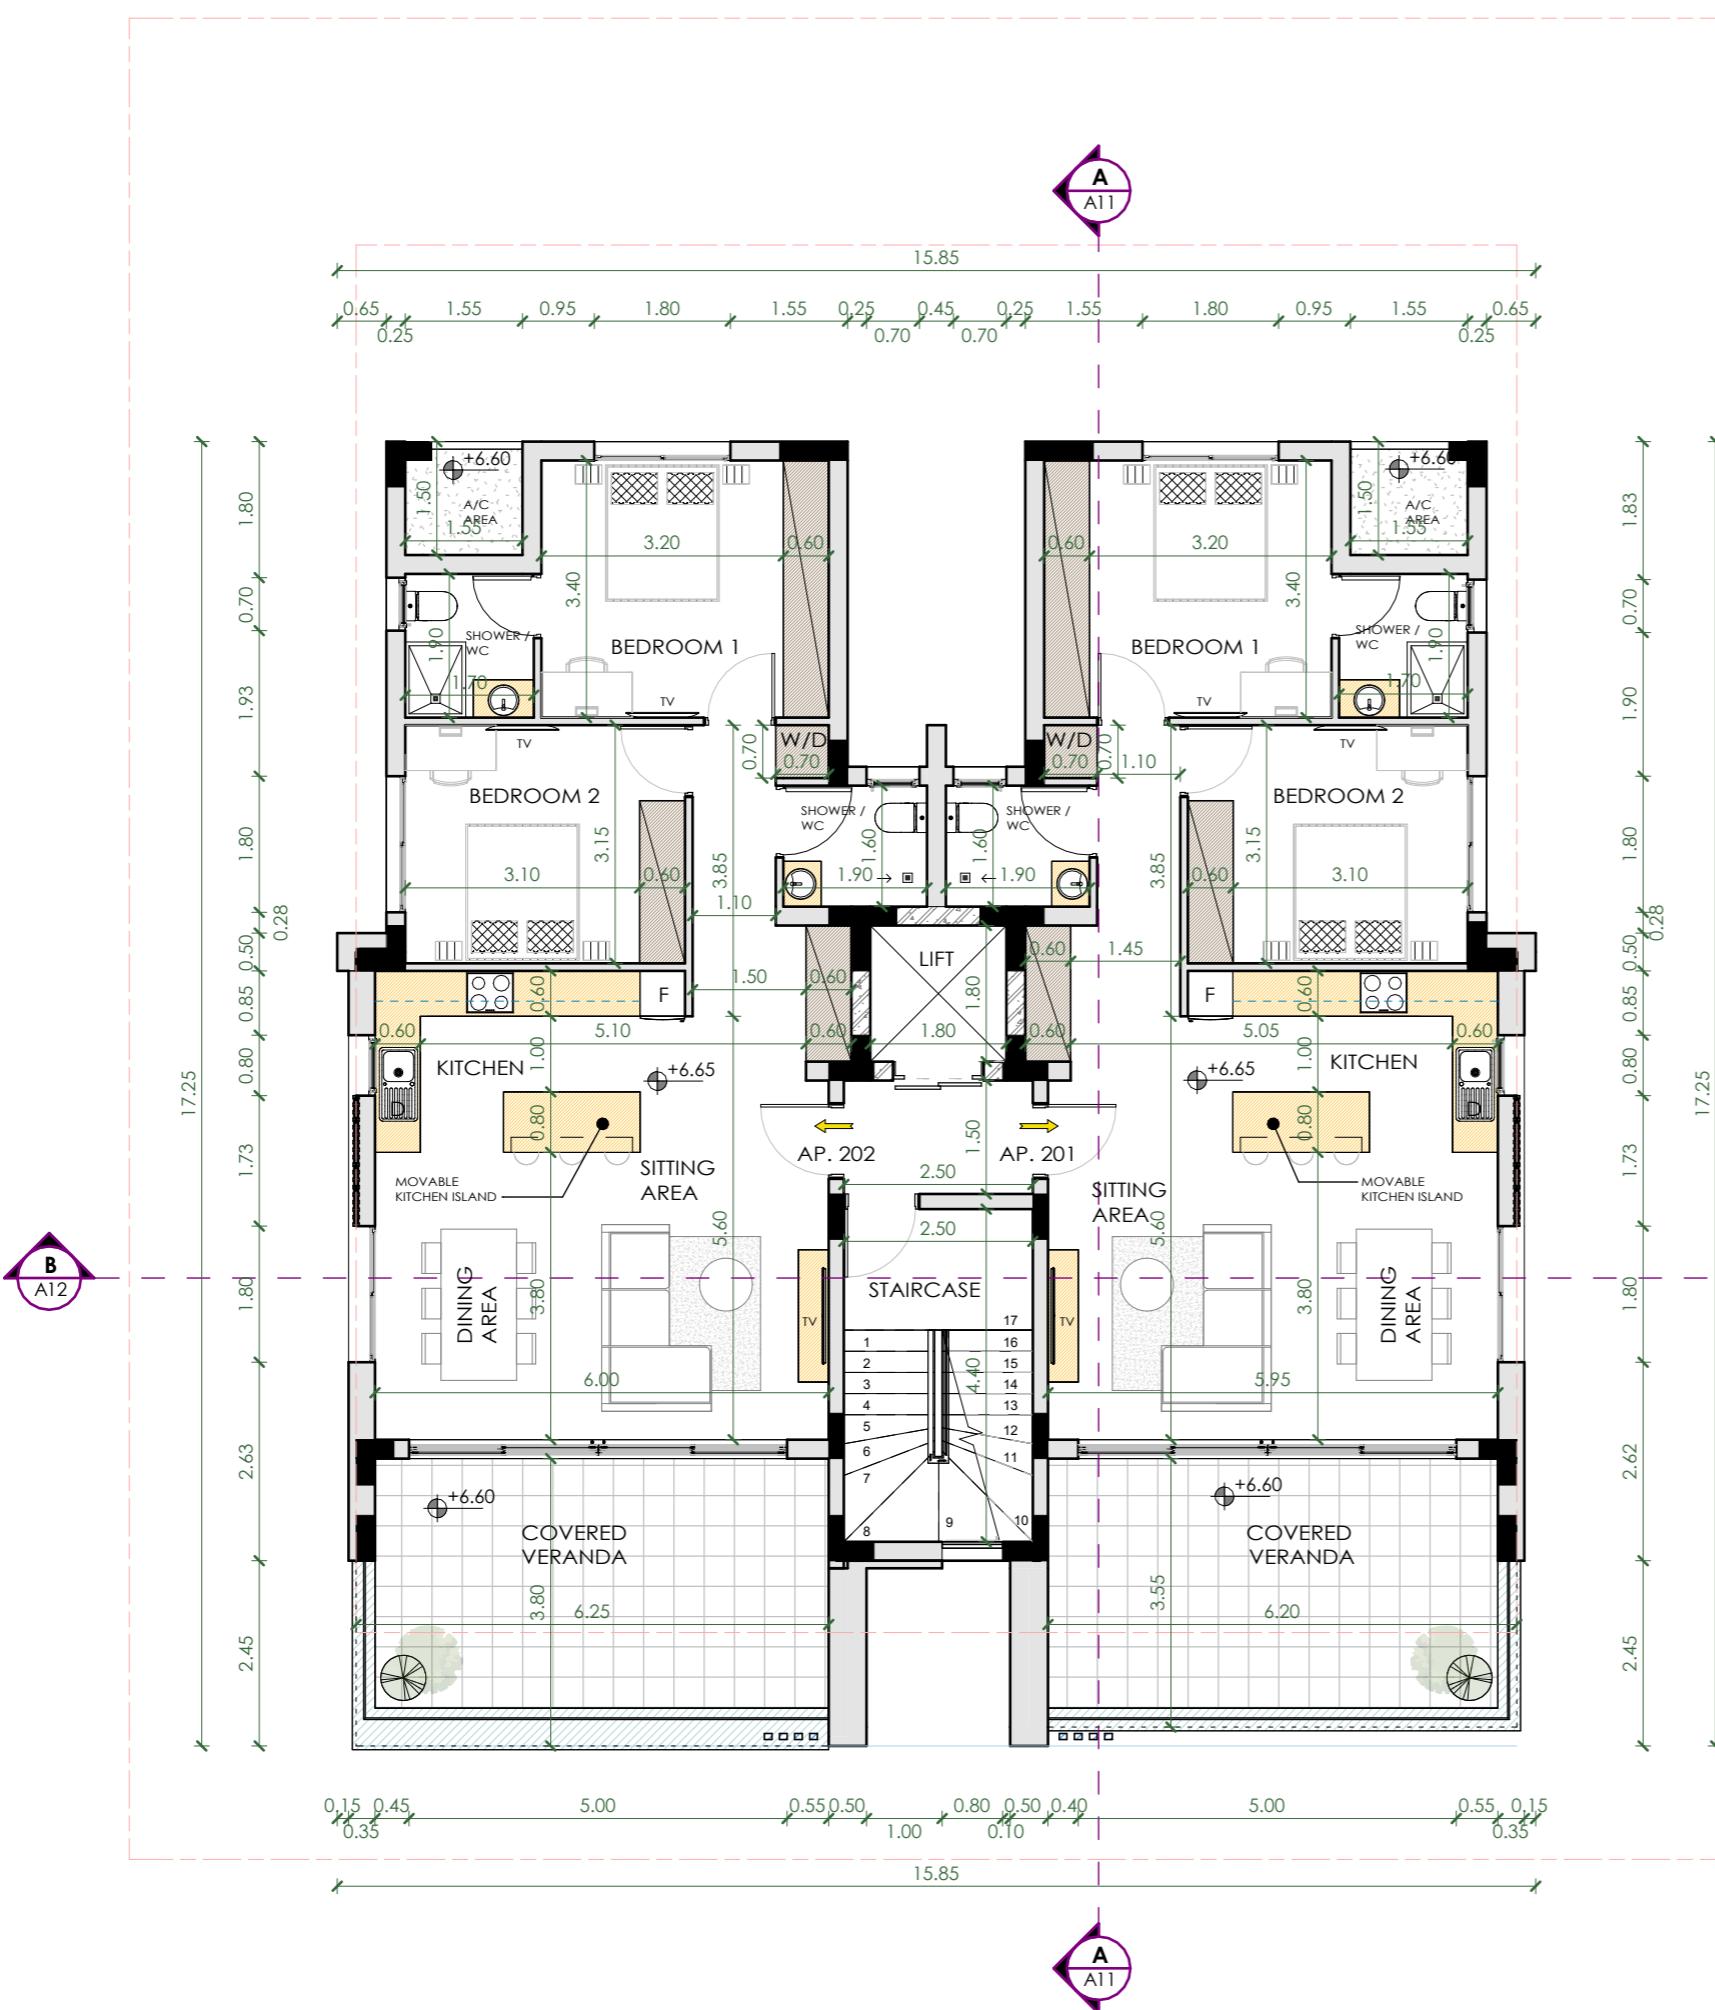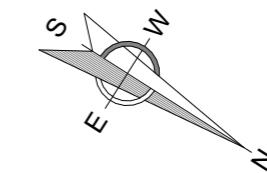

## SECOND FLOOR PLAN

1 : 100

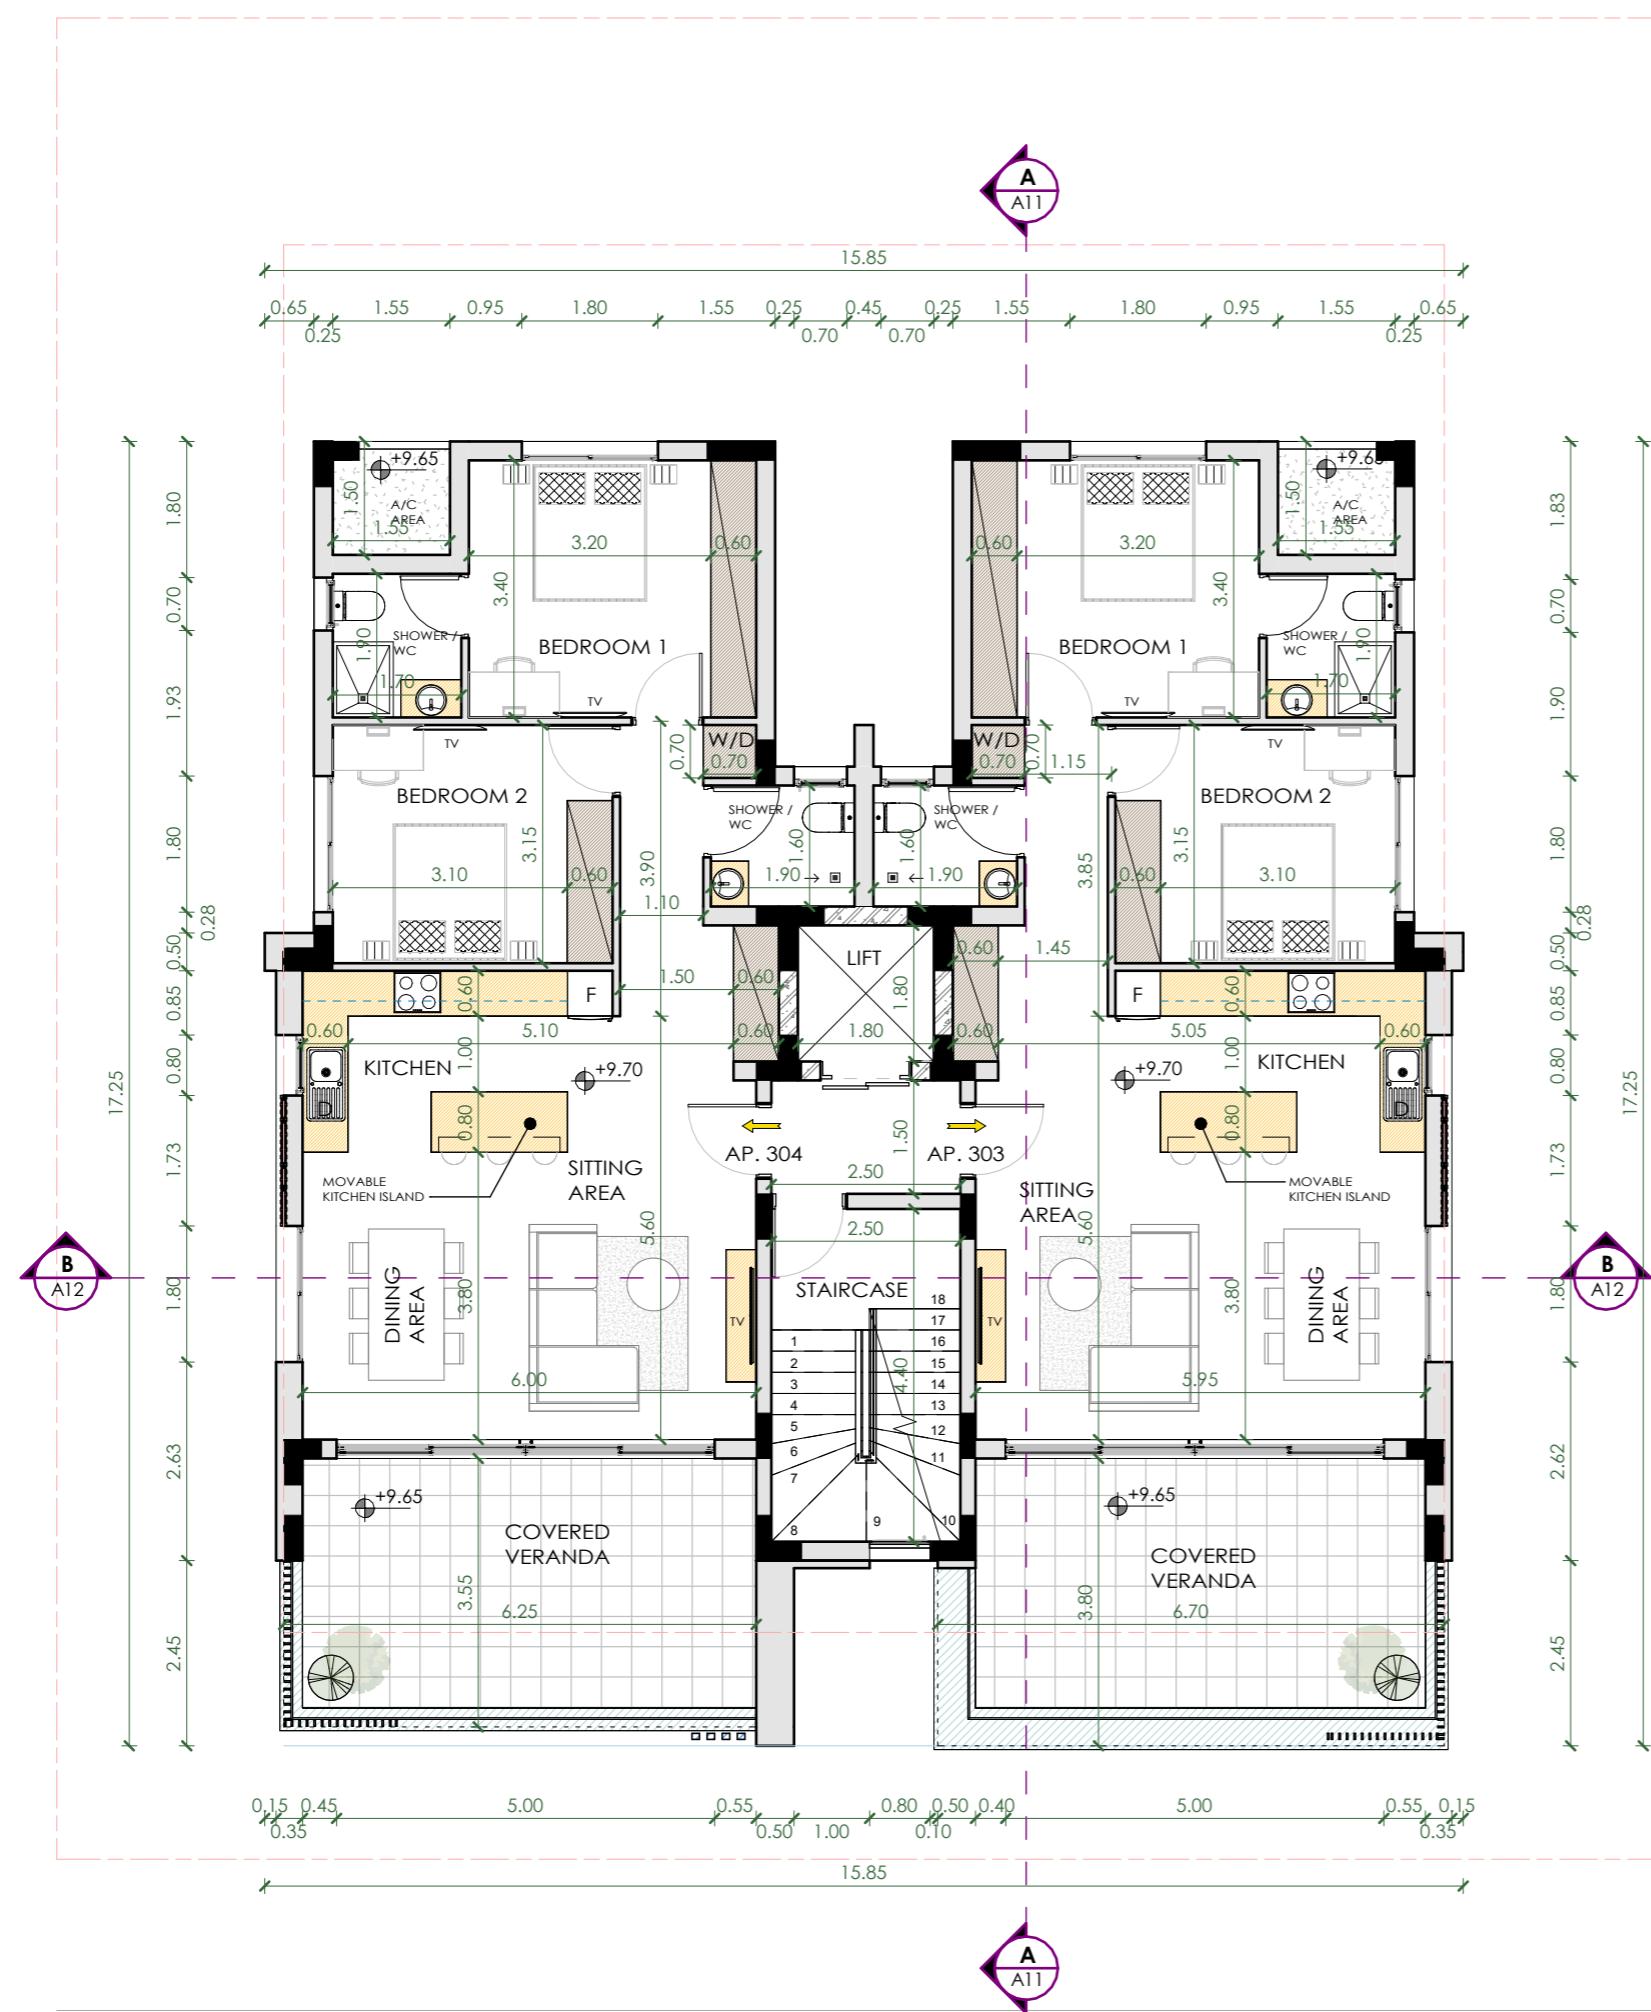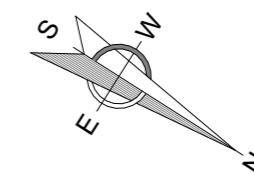

## THIRD FLOOR PLAN

1 : 100

Phones	Fax
+357 99 882907	+357 24 650846
+357 99 640508	

**Address**  
Nikodimou Milona 28,  
Sunorama House, off. 401,  
6050 Larnaka

**Email:**  
[info@cgpchristou.com](mailto:info@cgpchristou.com)

**Description**

**Client Name**  
PAPANTONIS NIKOLAIDIS

**City/Village**  
LIMASSOL / ZAKAKI

**Sheet Name**  
ROOF GARDEN FLOOR  
PLAN


**Project number**

**Date** 09/23

**Sheet number**

A5

**Scale** 1 : 100

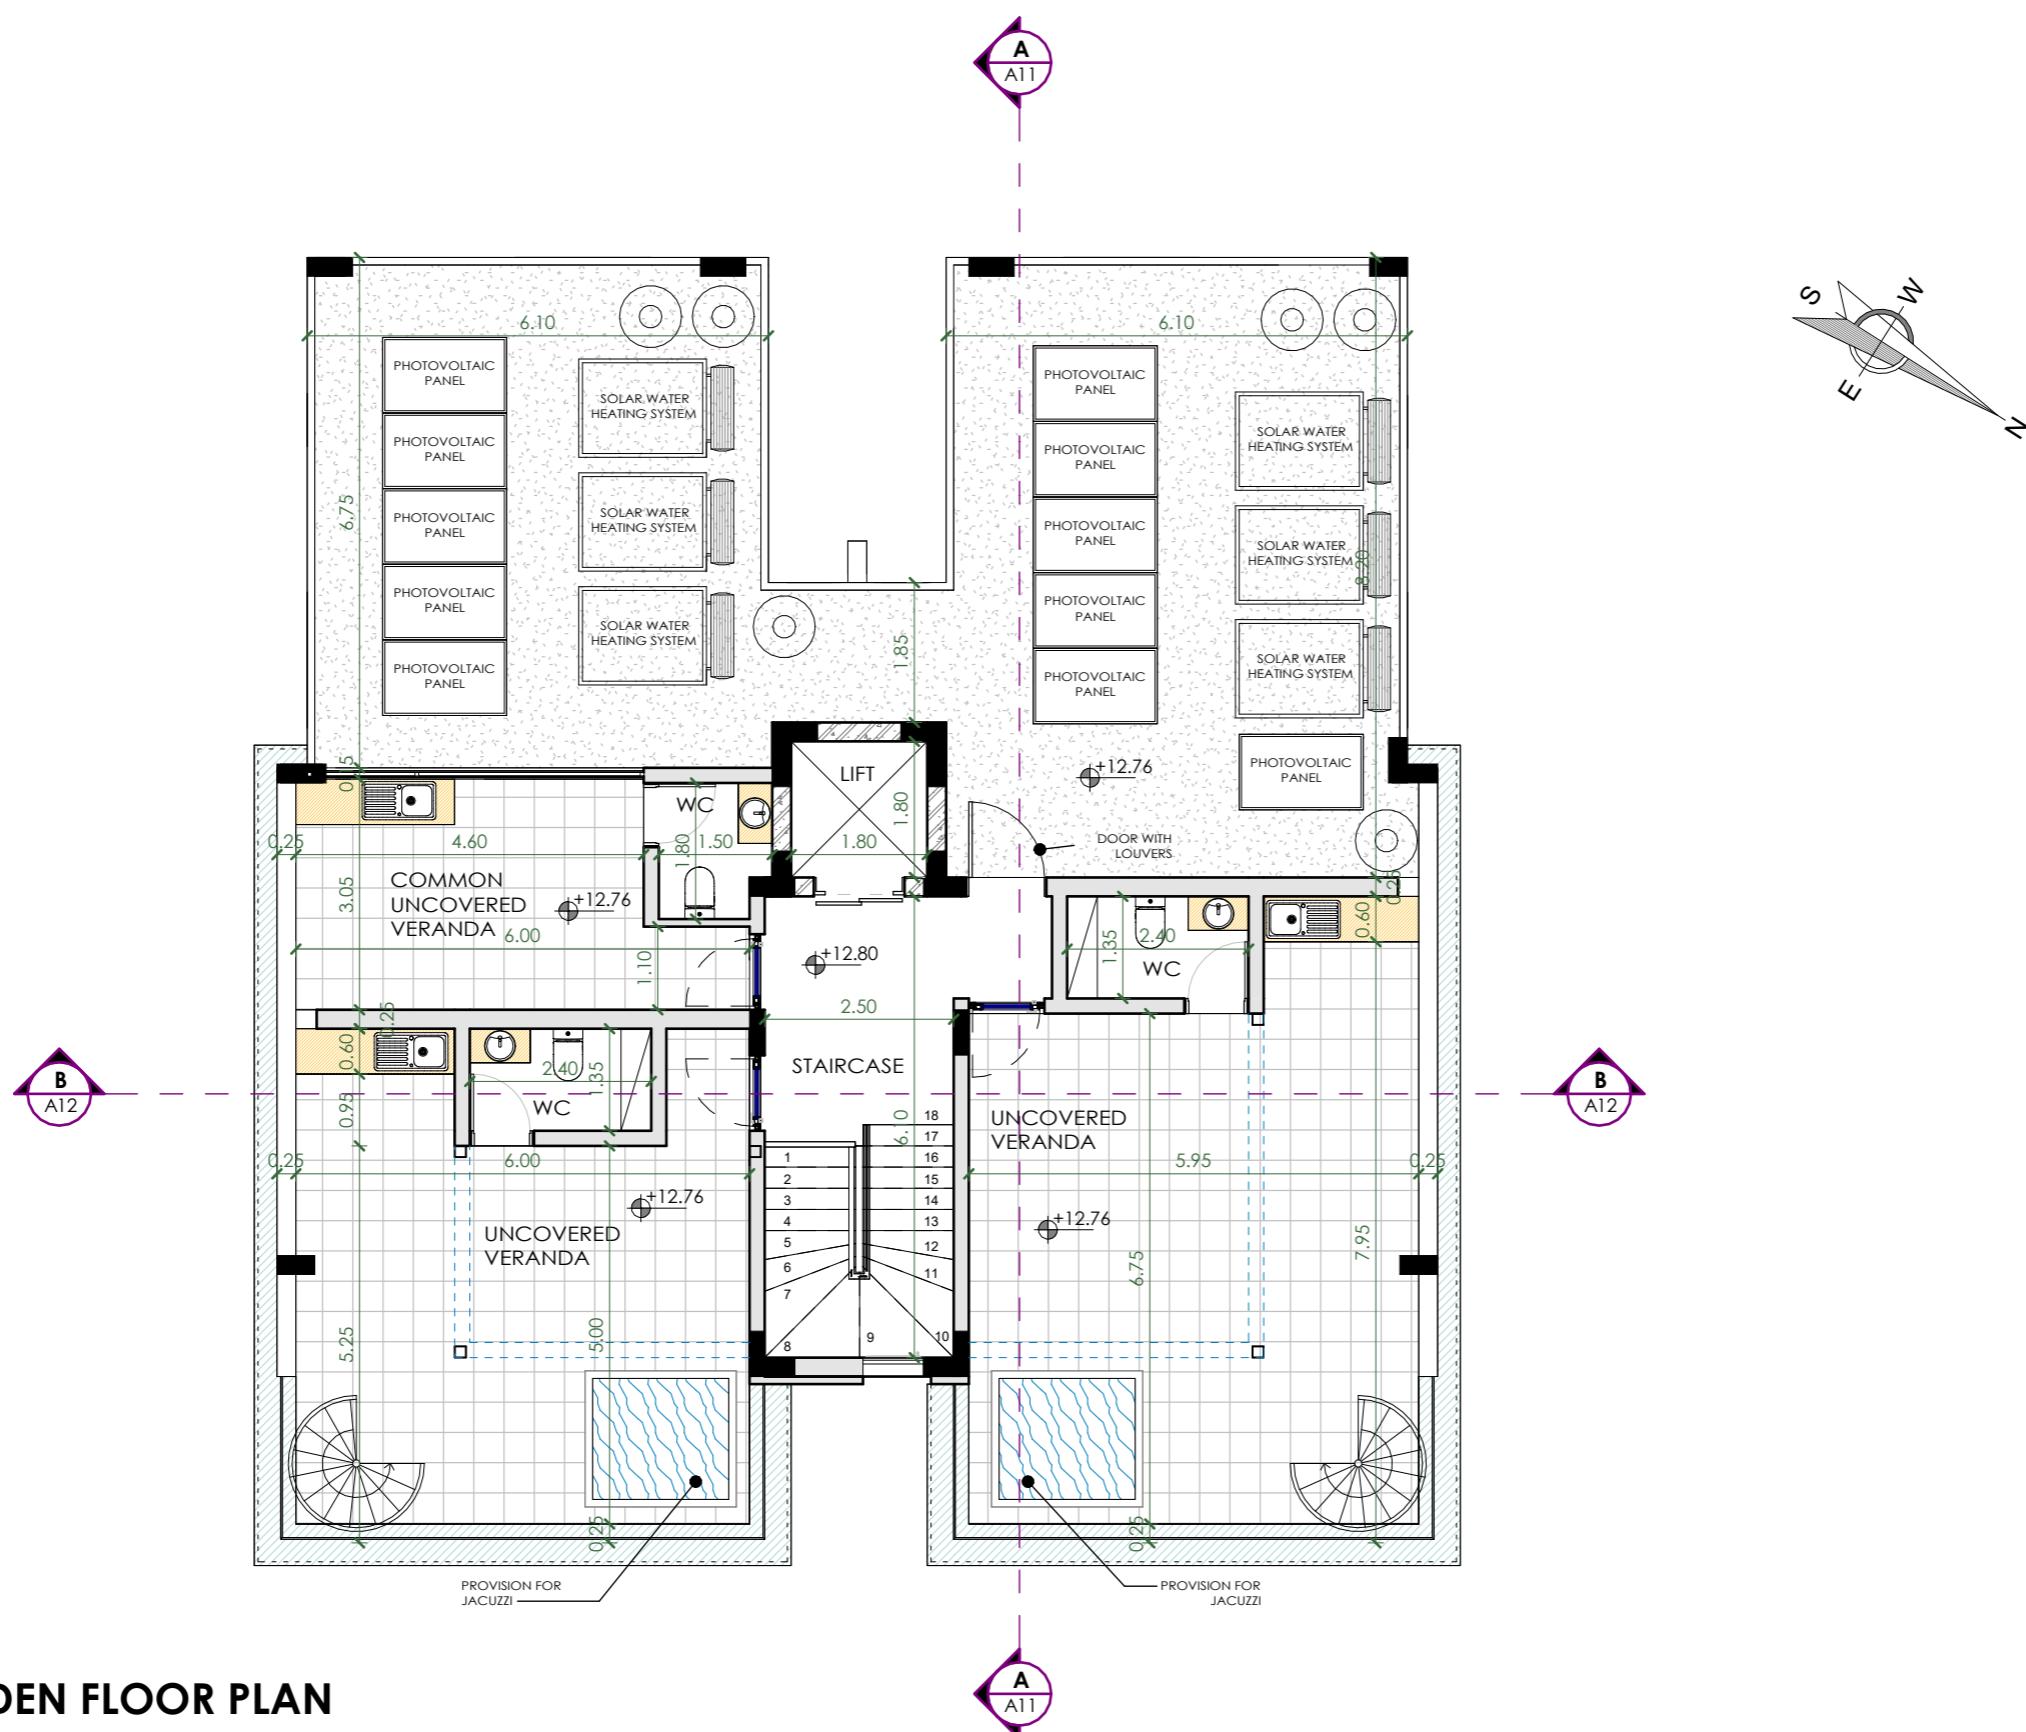

## ROOF GARDEN FLOOR PLAN

1 : 100



<b>Phones</b>	<b>Fax</b>
+357 99 882907	+357 24 650846
+357 99 640508	

**Address**  
Nikodimou Milona 28,  
Sunorama House, off. 401,  
6050 Larnaka

**Email:**  
[info@cgpchristou.com](mailto:info@cgpchristou.com)

**Description**

**Client Name**  
PAPANTONIS NIKOLAIDIS


**City/Village**  
LIMASSOL / ZAKAKI

**Sheet Name**  
ROOF FLOOR PLAN

**Project number**  
**Date** 09/23

**Sheet number**  
**A6**

**Scale** 1 : 100

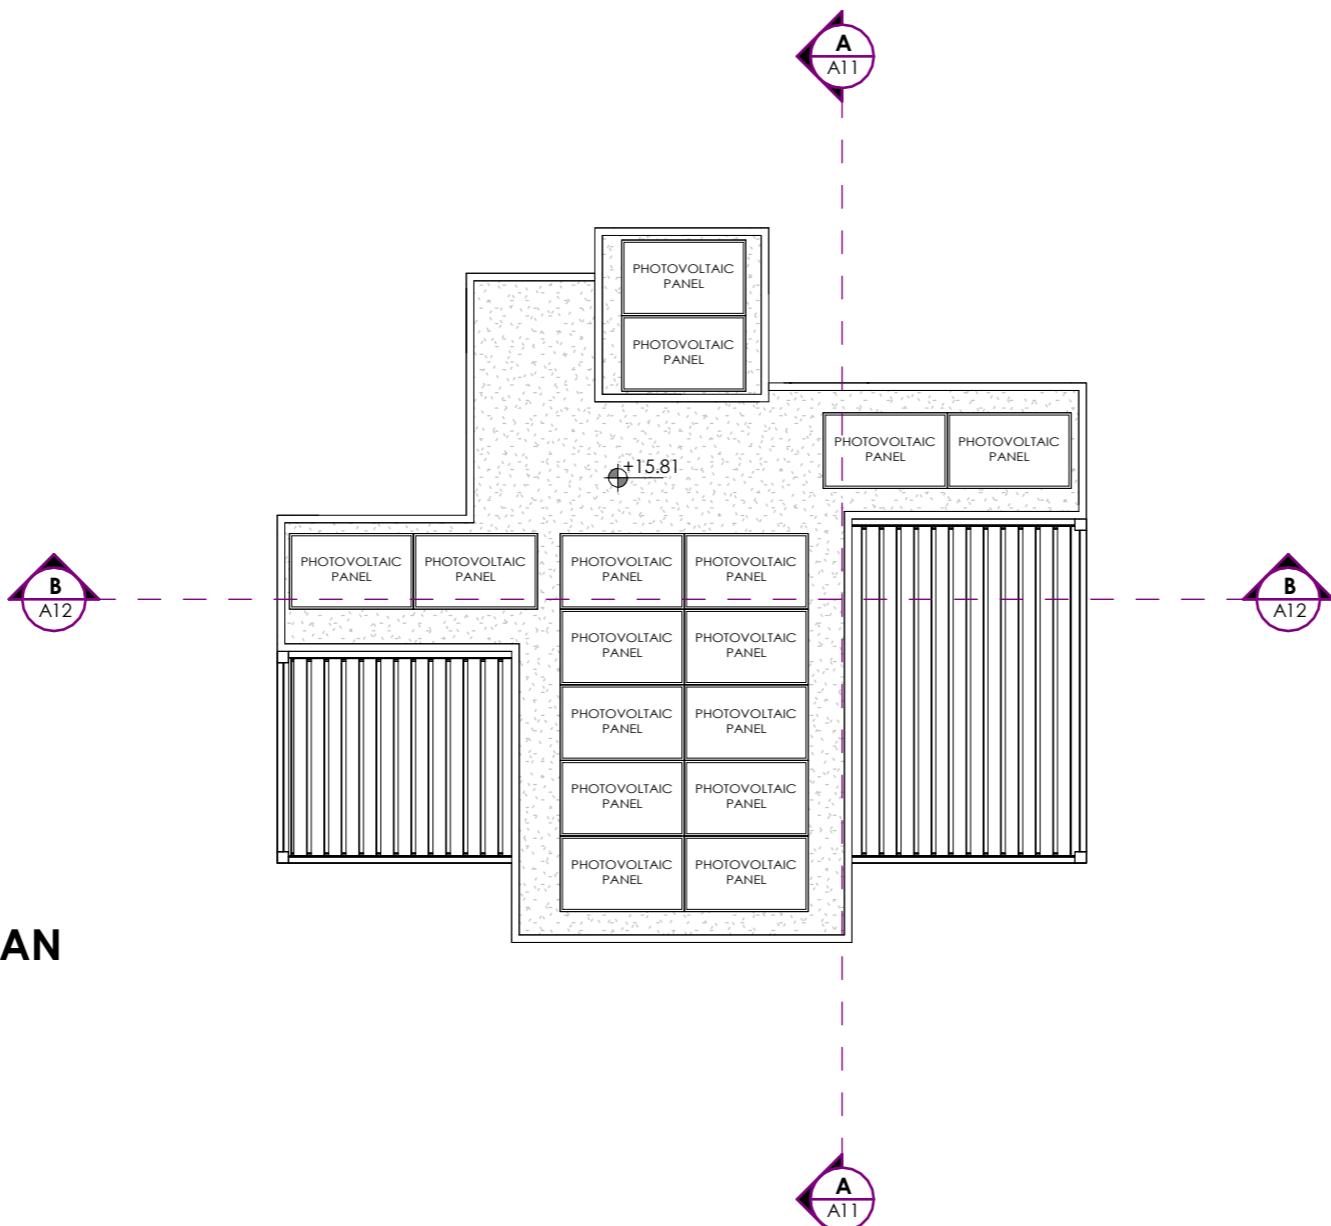

## ROOF FLOOR PLAN

1 : 100

Phones	Fax
+357 99 882907	+357 24 650846
+357 99 640508	

**Address**  
Nikodimou Milona 28,  
Sunorama House, off. 401,  
6050 Larnaka

**Email:**  
[info@cgchristou.com](mailto:info@cgchristou.com)

**Description**

**Client Name**  
PAPANTONIS NIKOLAIDIS

**City/Village**  
LIMASSOL / ZAKAKI

**Sheet Name**  
FRONT VIEW

**Project number**

**Date** 09/23

**Sheet number**

A7

**Scale** 1 : 100





Phones	Fax
+357 99 882907	+357 24 650846
+357 99 640508	

**Address**  
Nikodimou Milona 28,  
Sunorama House, off. 401,  
6050 Larnaka

**Email:**  
[info@cgpchristou.com](mailto:info@cgpchristou.com)

**Description**

**Client Name**  
PAPANTONIS NIKOLAIDIS

**City/Village**  
LIMASSOL / ZAKAKI

**Sheet Name**  
BACK VIEW


**Project number**

**Date** 09/23

**Sheet number**

A8

**Scale** 1 : 100

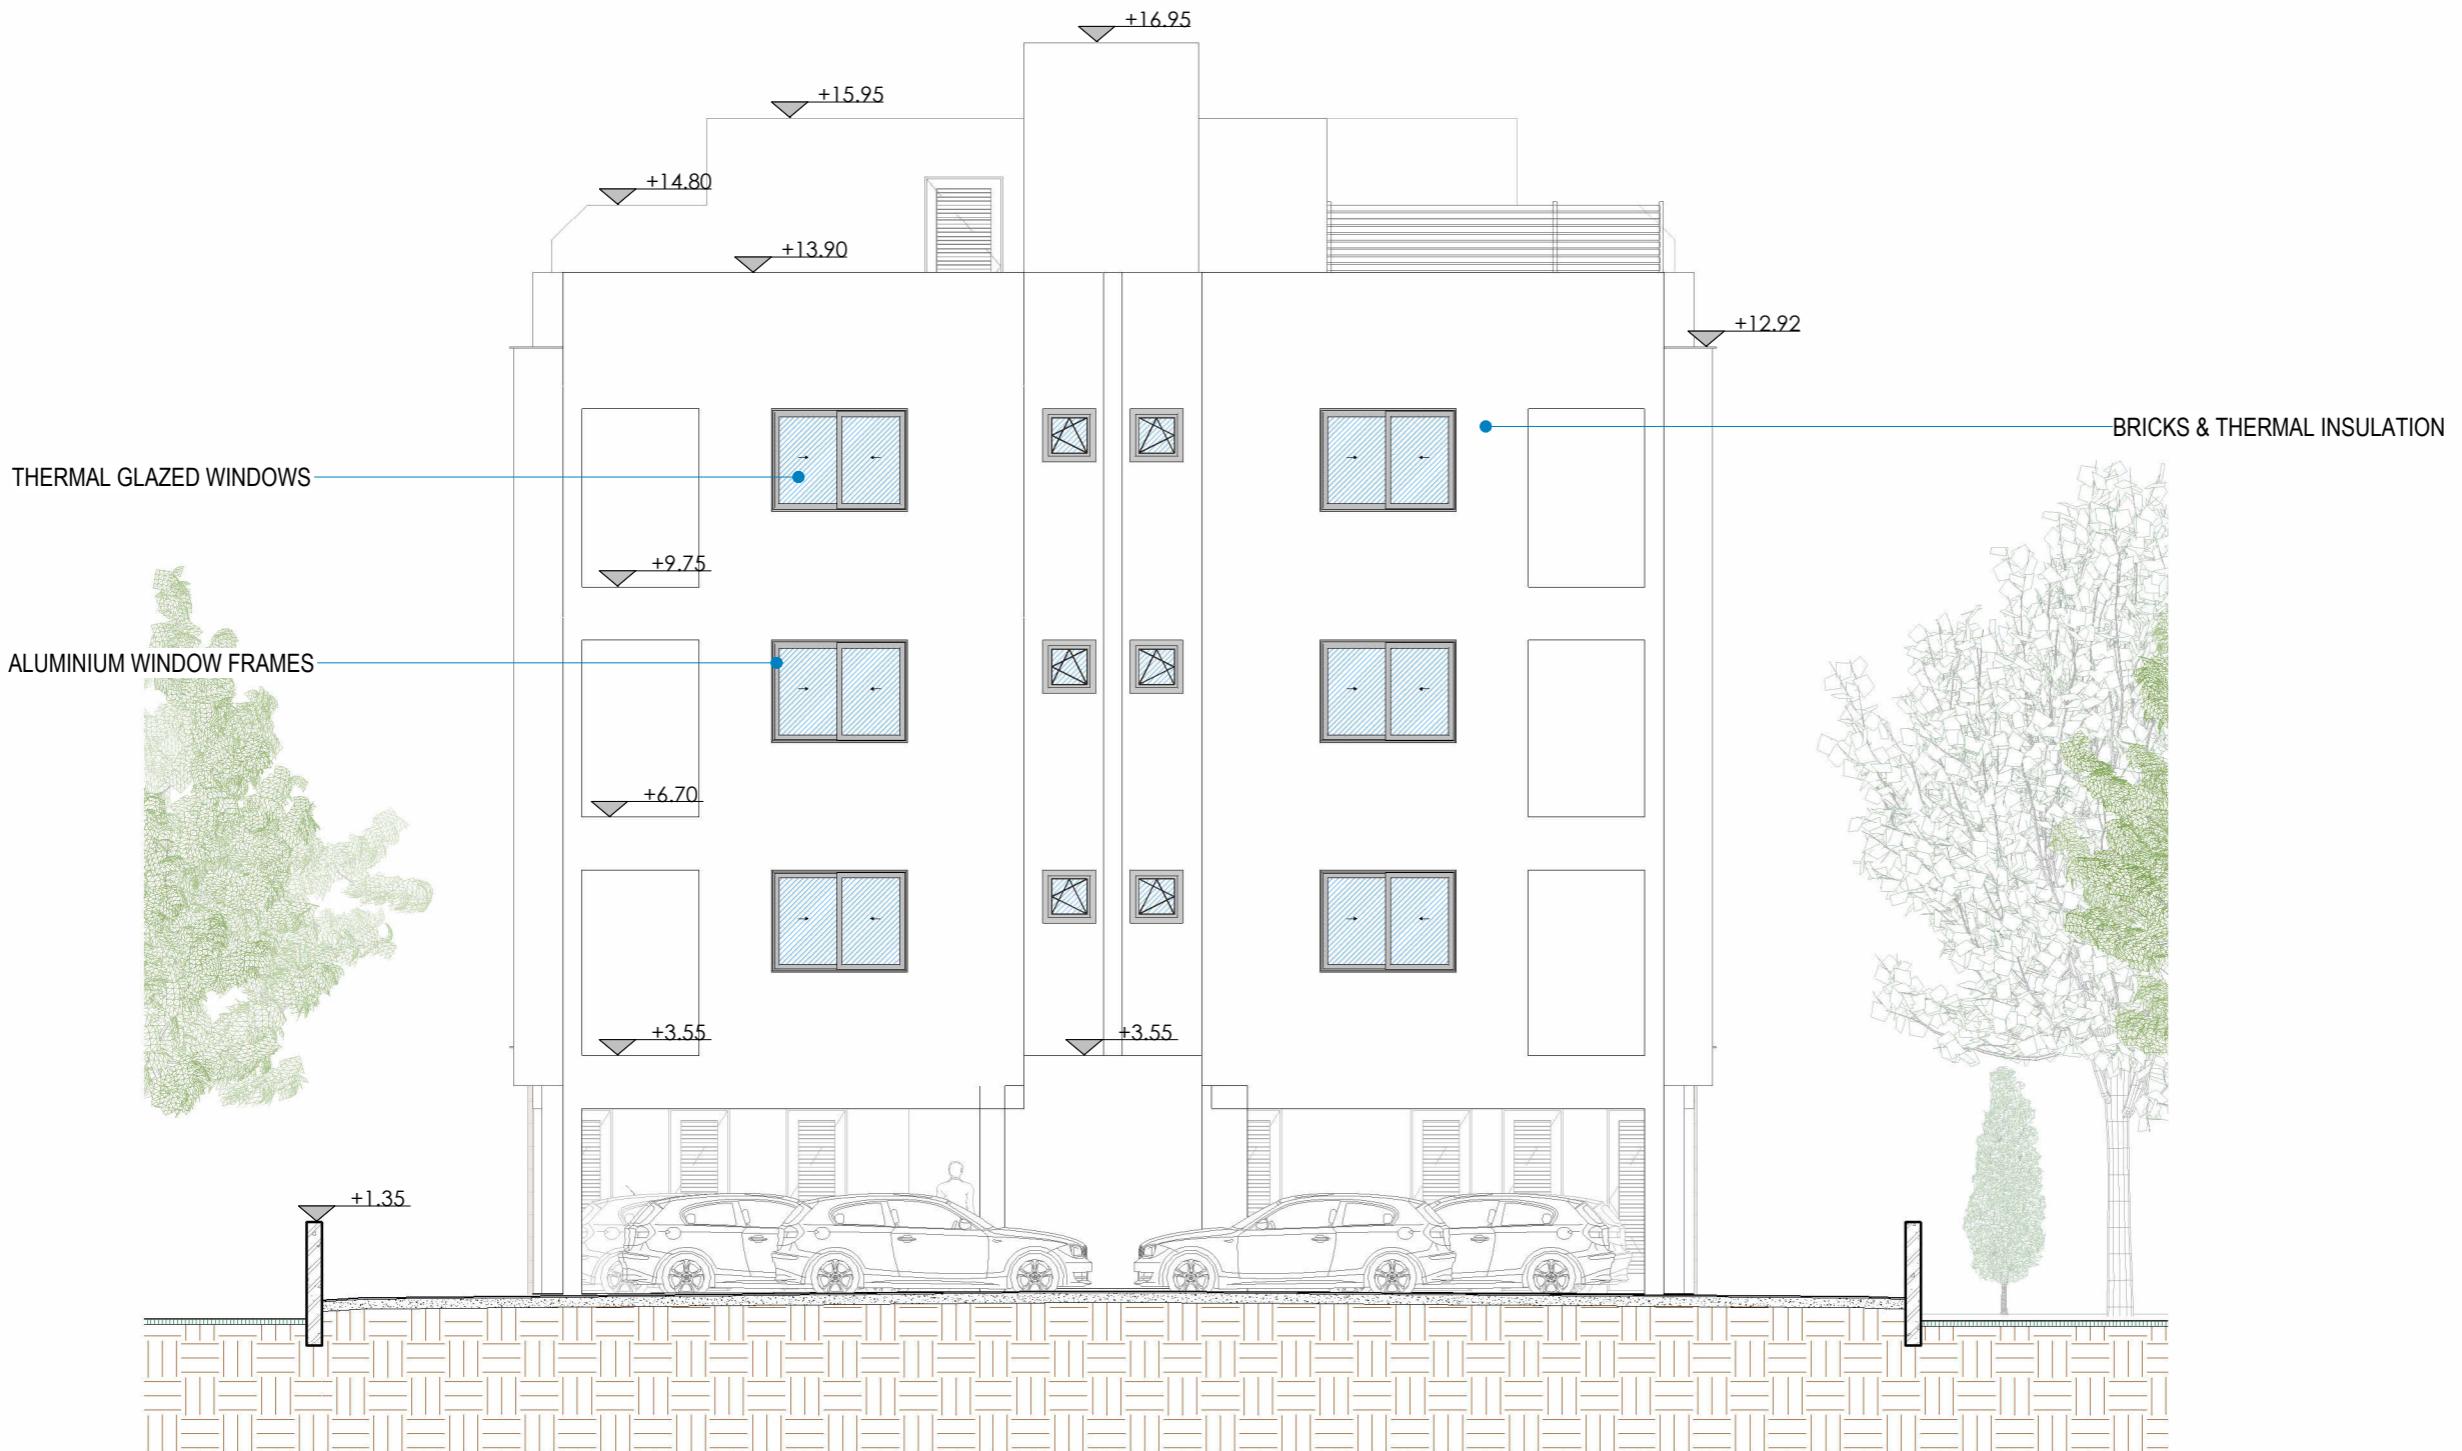

**BACK VIEW**

1 : 100



**Phones** +357 99 882907  
**Fax** +357 24 650846  
+357 99 640508

**Address**  
Nikodimou Milona 28,  
Sunorama House, off. 401,  
6050 Larnaka

**Email:** [info@cgpchristou.com](mailto:info@cgpchristou.com)

**Description**

**Client Name**  
PAPANTONIS NIKOLAIDIS

**City/Village**  
LIMASSOL / ZAKAKI

**Sheet Name**  
SIDE VIEW A


**Project number**

**Date** 09/23

**Sheet number**

A9

**Scale** 1 : 100

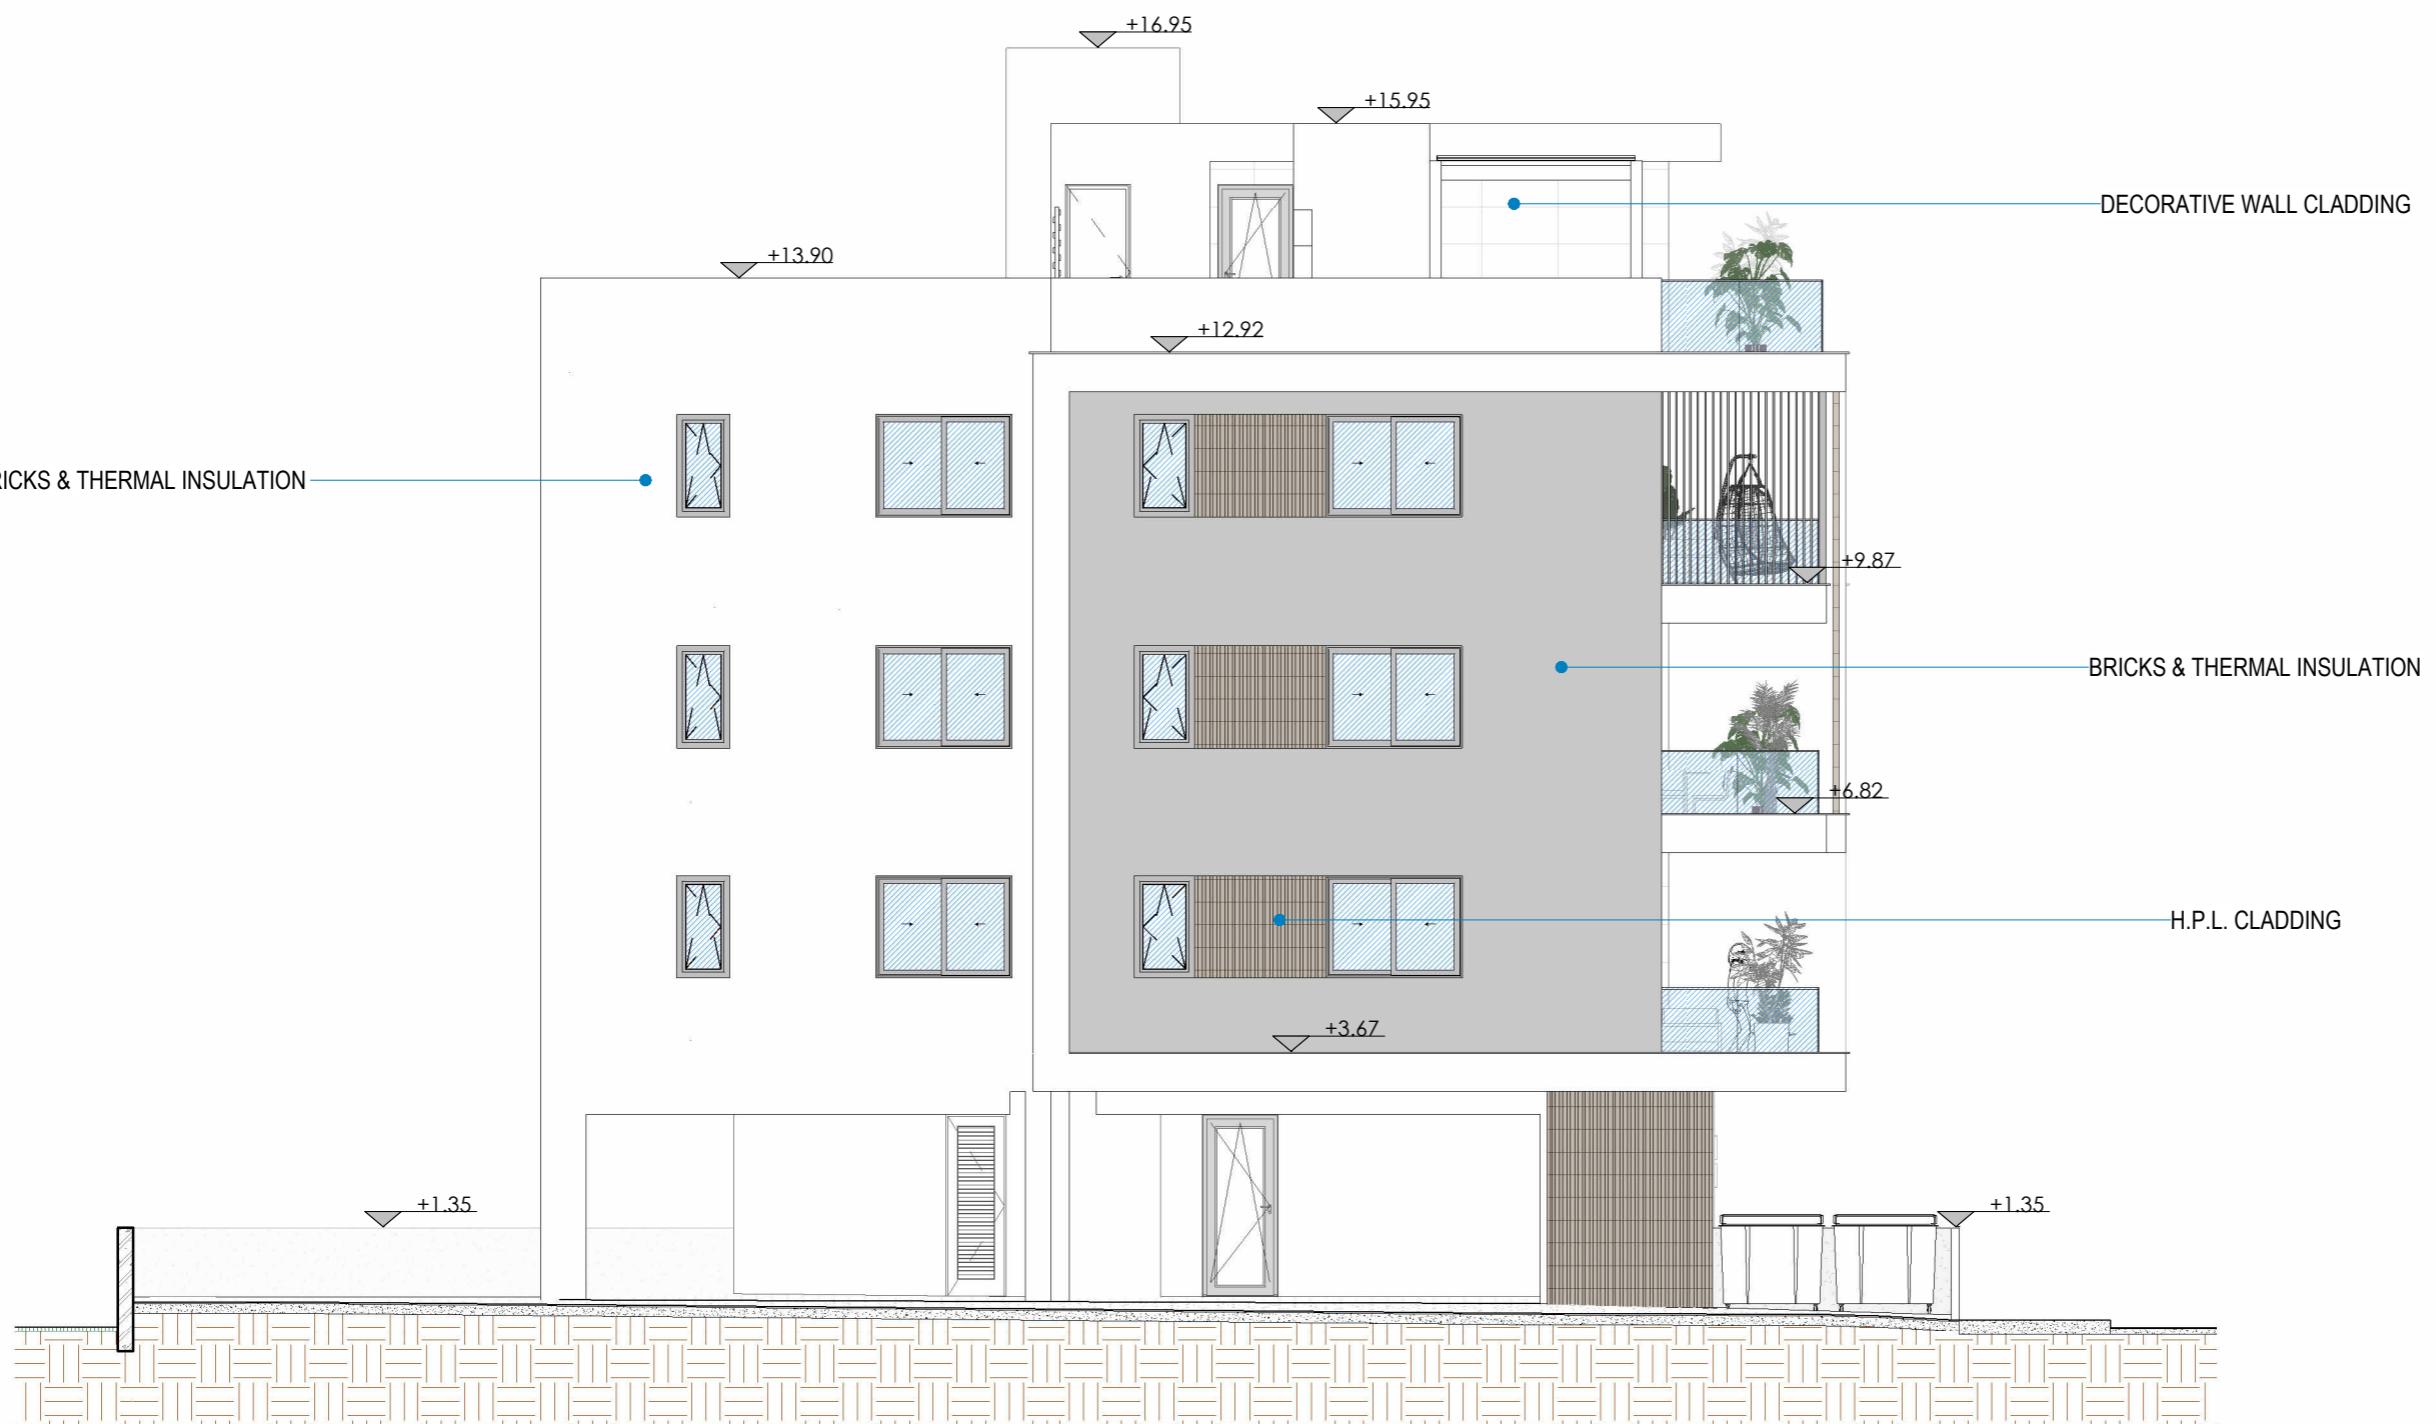




**Phones** +357 99 882907  
**Fax** +357 24 650846  
+357 99 640508

**Address**  
Nikodimou Milona 28,  
Sunorama House, off. 401,  
6050 Larnaka

**Email:** [info@cgchristou.com](mailto:info@cgchristou.com)

**Description**

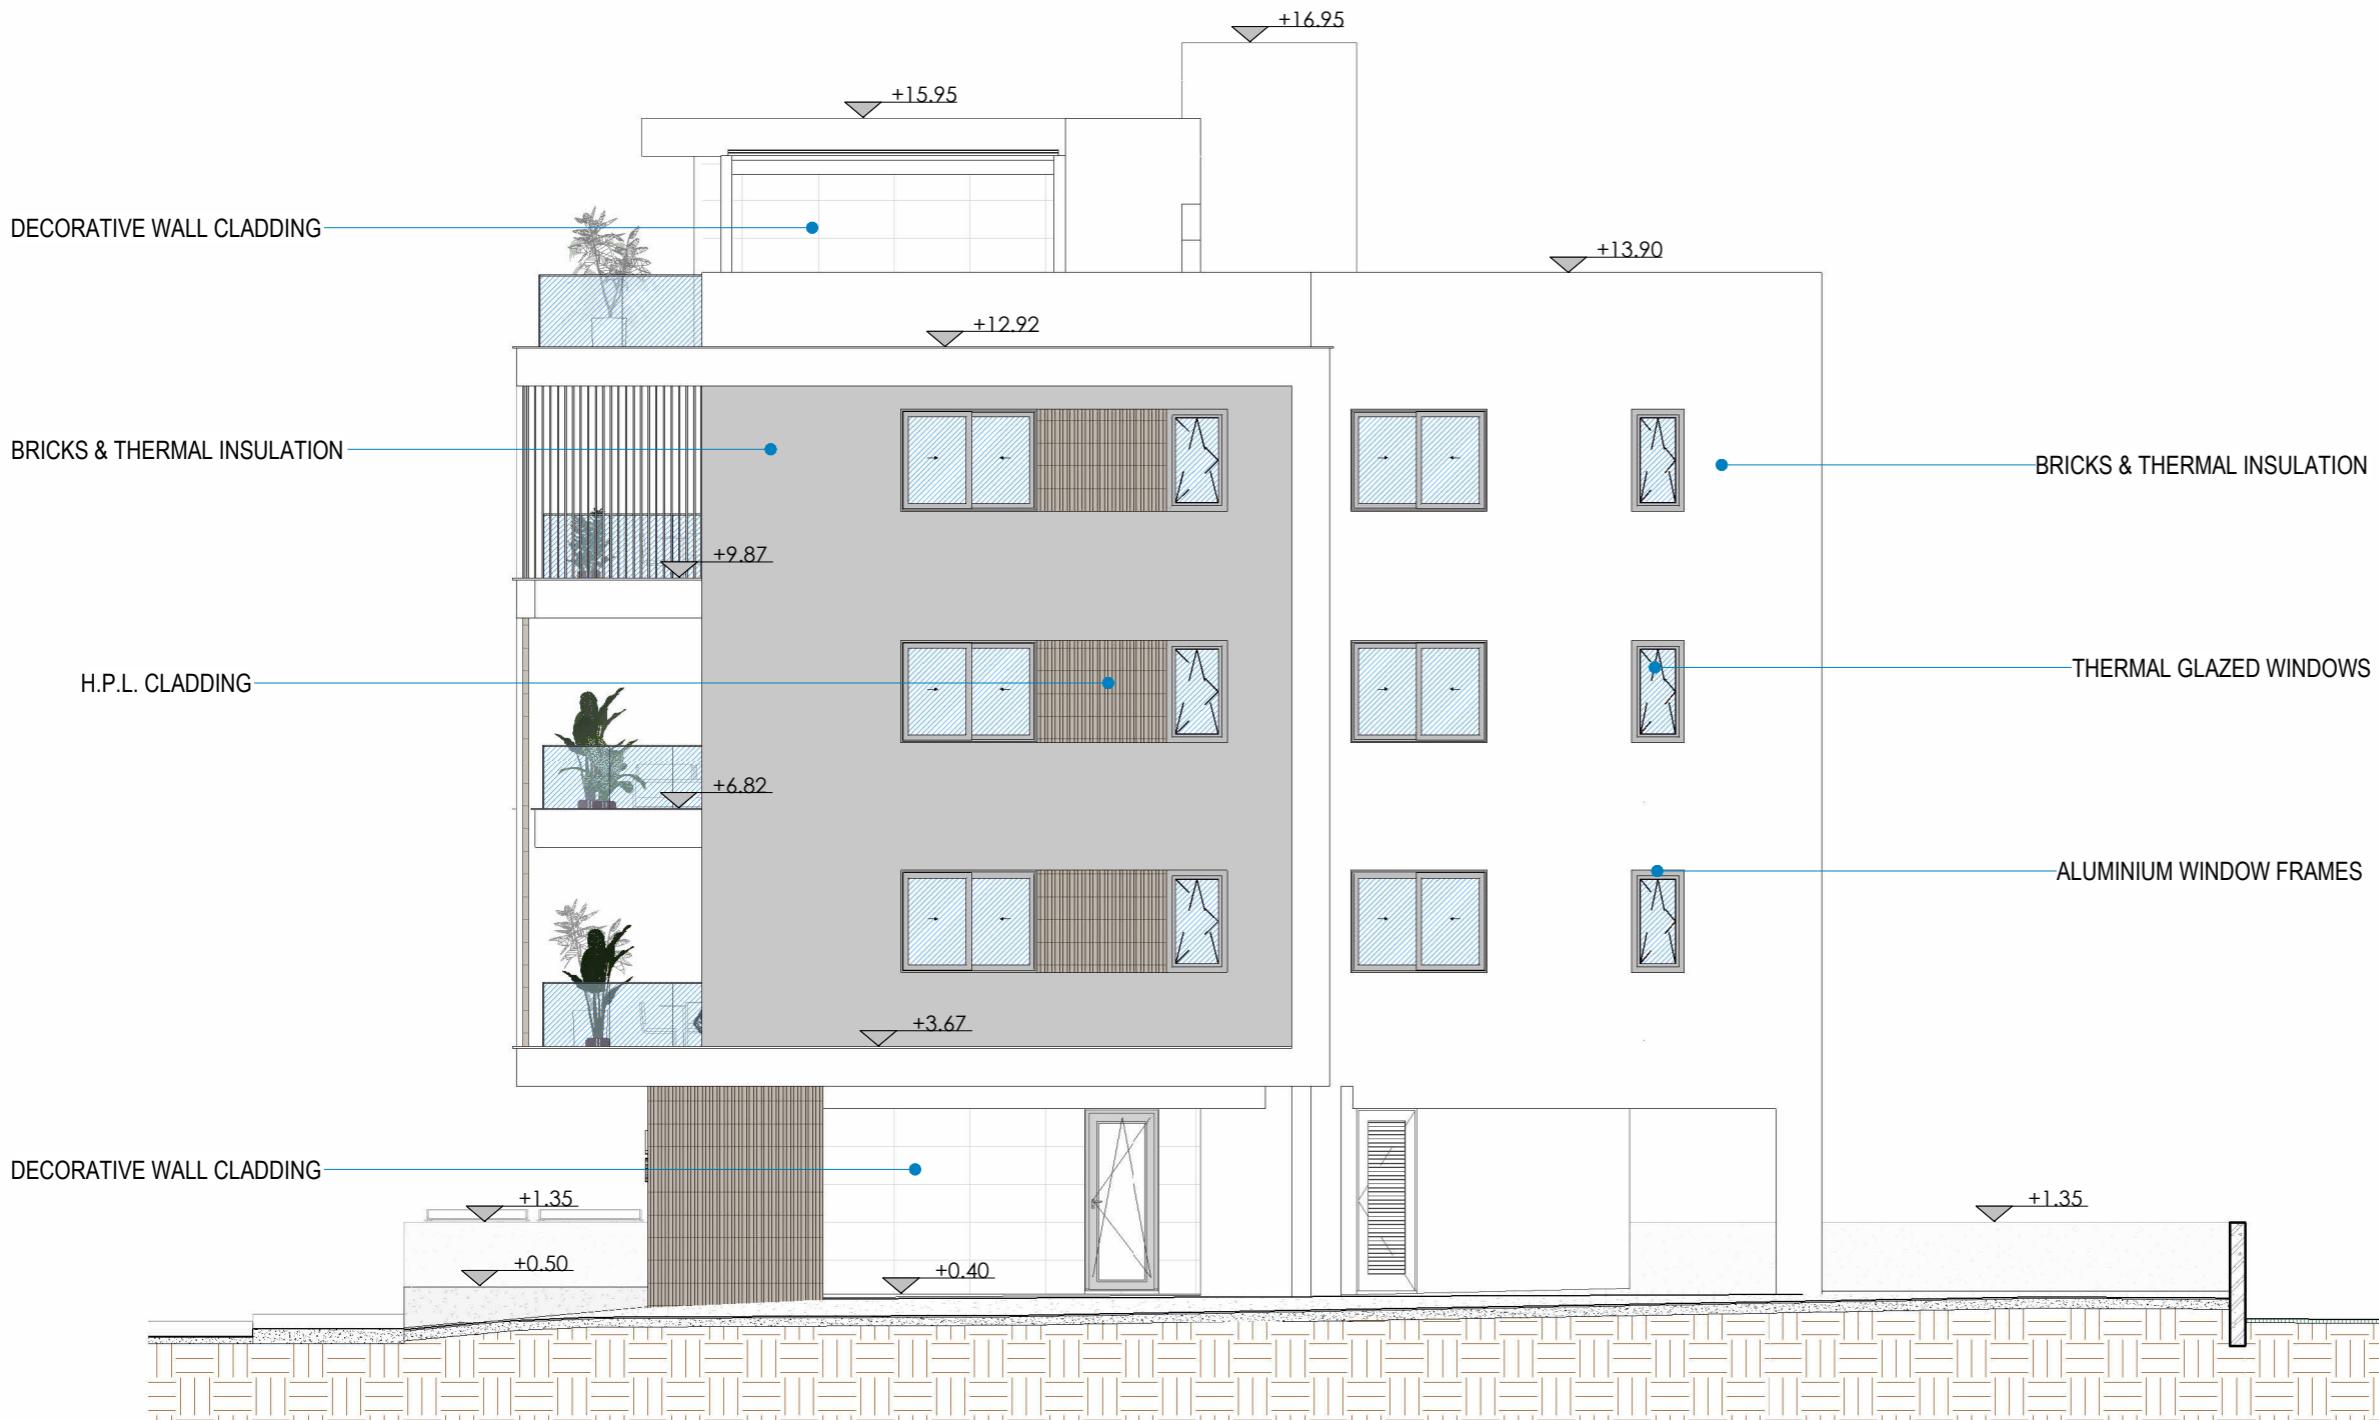

**SIDE VIEW B**

1 : 100

A10

**Project number** 09/23  
**Date** 09/23  
**Sheet number**  
**Scale** 1 : 100

**Client Name**  
PAPANTONIS NIKOLAIDIS

**City/Village**  
LIMASSOL / ZAKAKI

**Sheet Name**  
SIDE VIEW B

Phones	Fax
+357 99 882907	+357 24 650846
+357 99 640508	

**Address**  
Nikodimou Milona 28,  
Sunorama House, off. 401,  
6050 Larnaka

**Email:**  
[info@cgchristou.com](mailto:info@cgchristou.com)

**Description**

**Client Name**  
PAPANTONIS NIKOLAIDIS

**City/Village**  
LIMASSOL / ZAKAKI

**Sheet Name**  
SECTION A-A


**Project number**

**Date** 09/23

**Sheet number**

**A11**

**Scale** 1 : 100

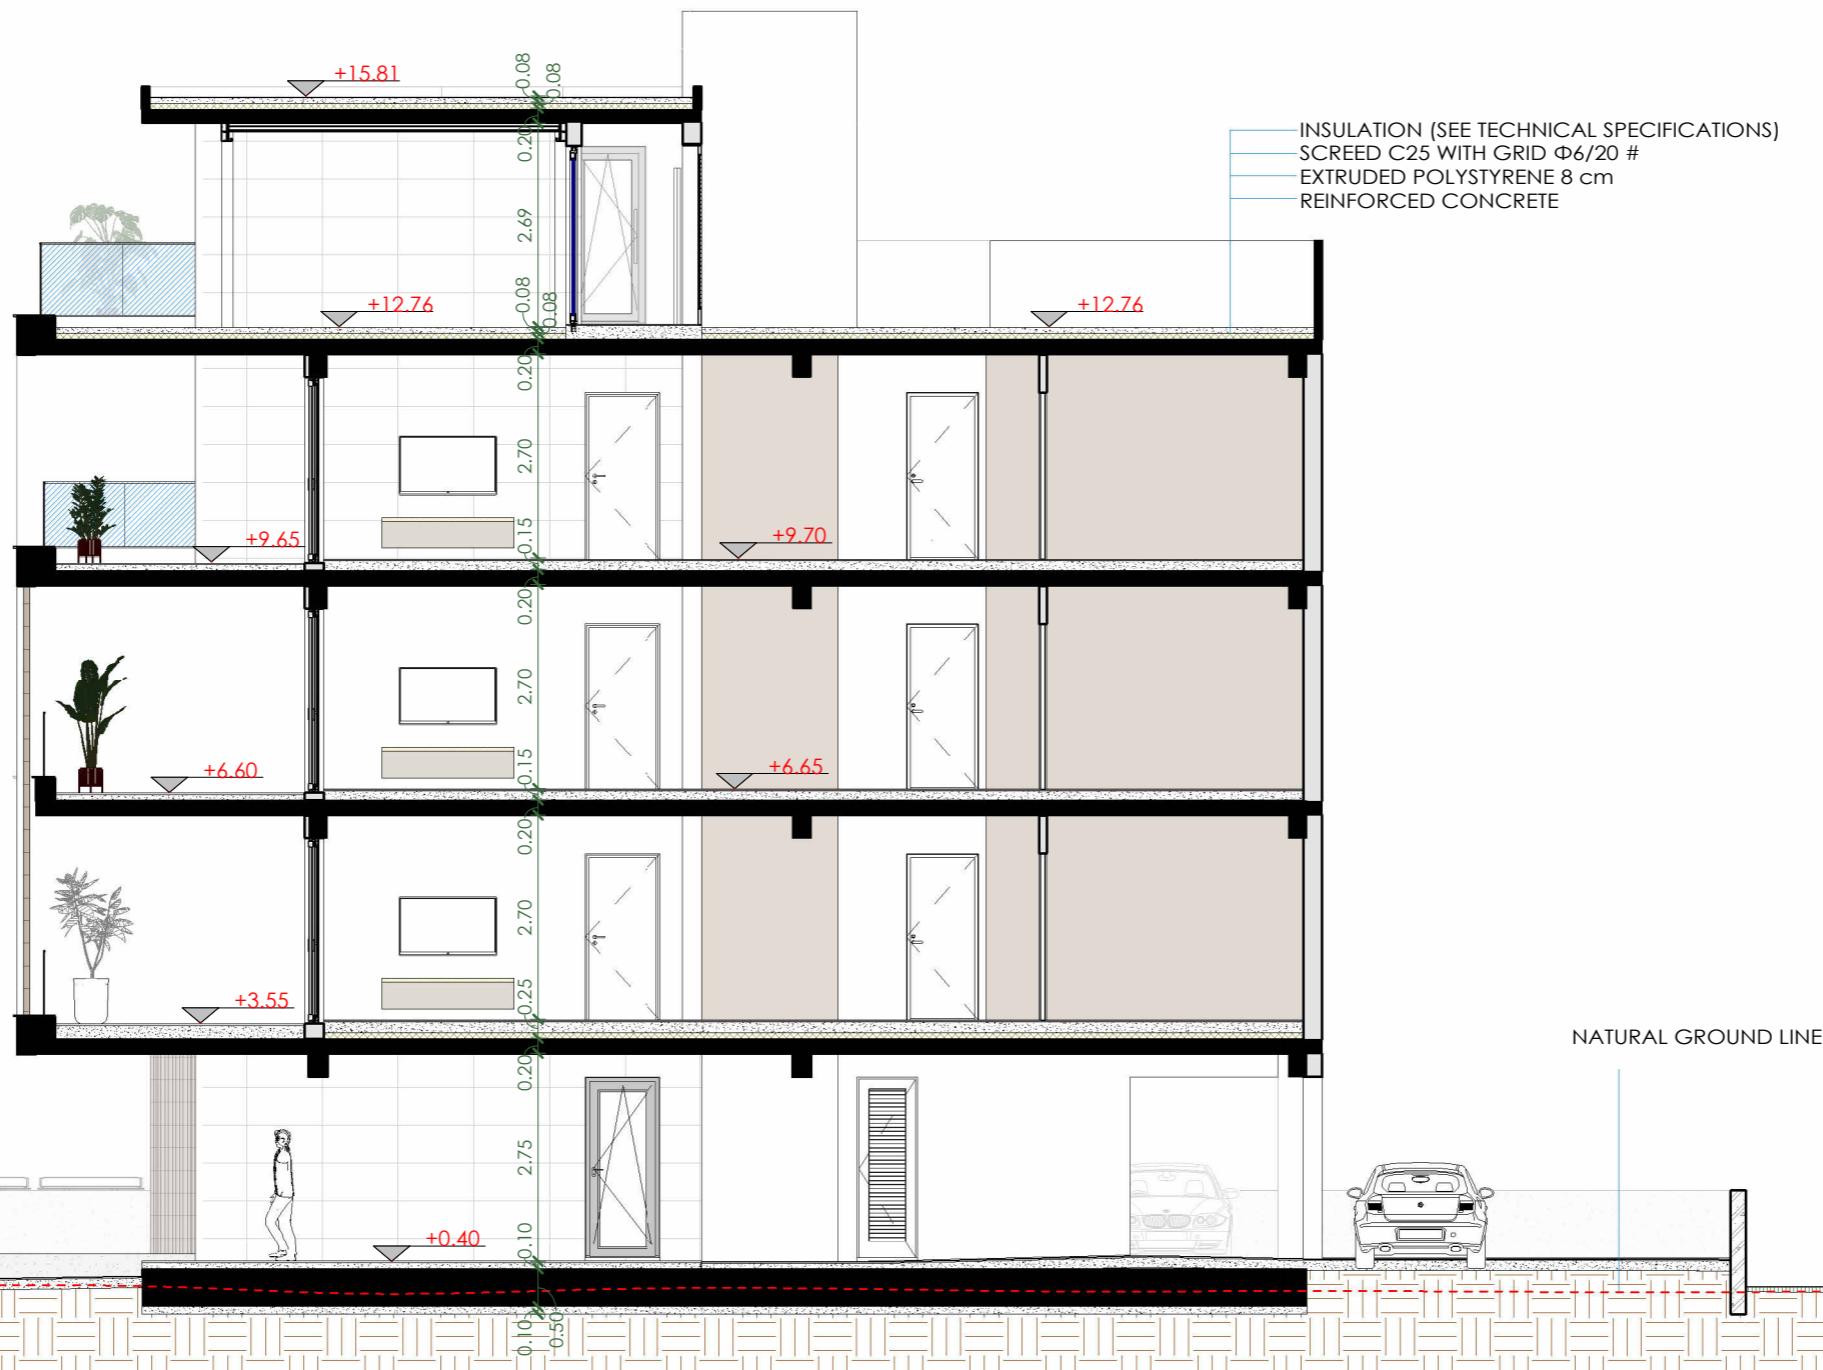

**SECTION A-A**

1 : 100



CHRISTOS  
CHRISTOU  
architecture studio

[www.cgpcchristou.com](http://www.cgpcchristou.com)



**Phones** +357 99 882907  
**Fax** +357 24 650846  
+357 99 640508

**Address**  
Nikodimou Milona 28,  
Sunorama House, off. 401,  
6050 Larnaka

**Email:** [info@cgpchristou.com](mailto:info@cgpchristou.com)

**Description**

**Client Name**  
PAPANTONIS NIKOLAIDIS

**City/Village**  
LIMASSOL / ZAKAKI

**Sheet Name**  
GROUND FLOOR AREA  
PLAN


**Project number**

**Date** 09/23

**Sheet number**

E1

**Scale** 1 : 100

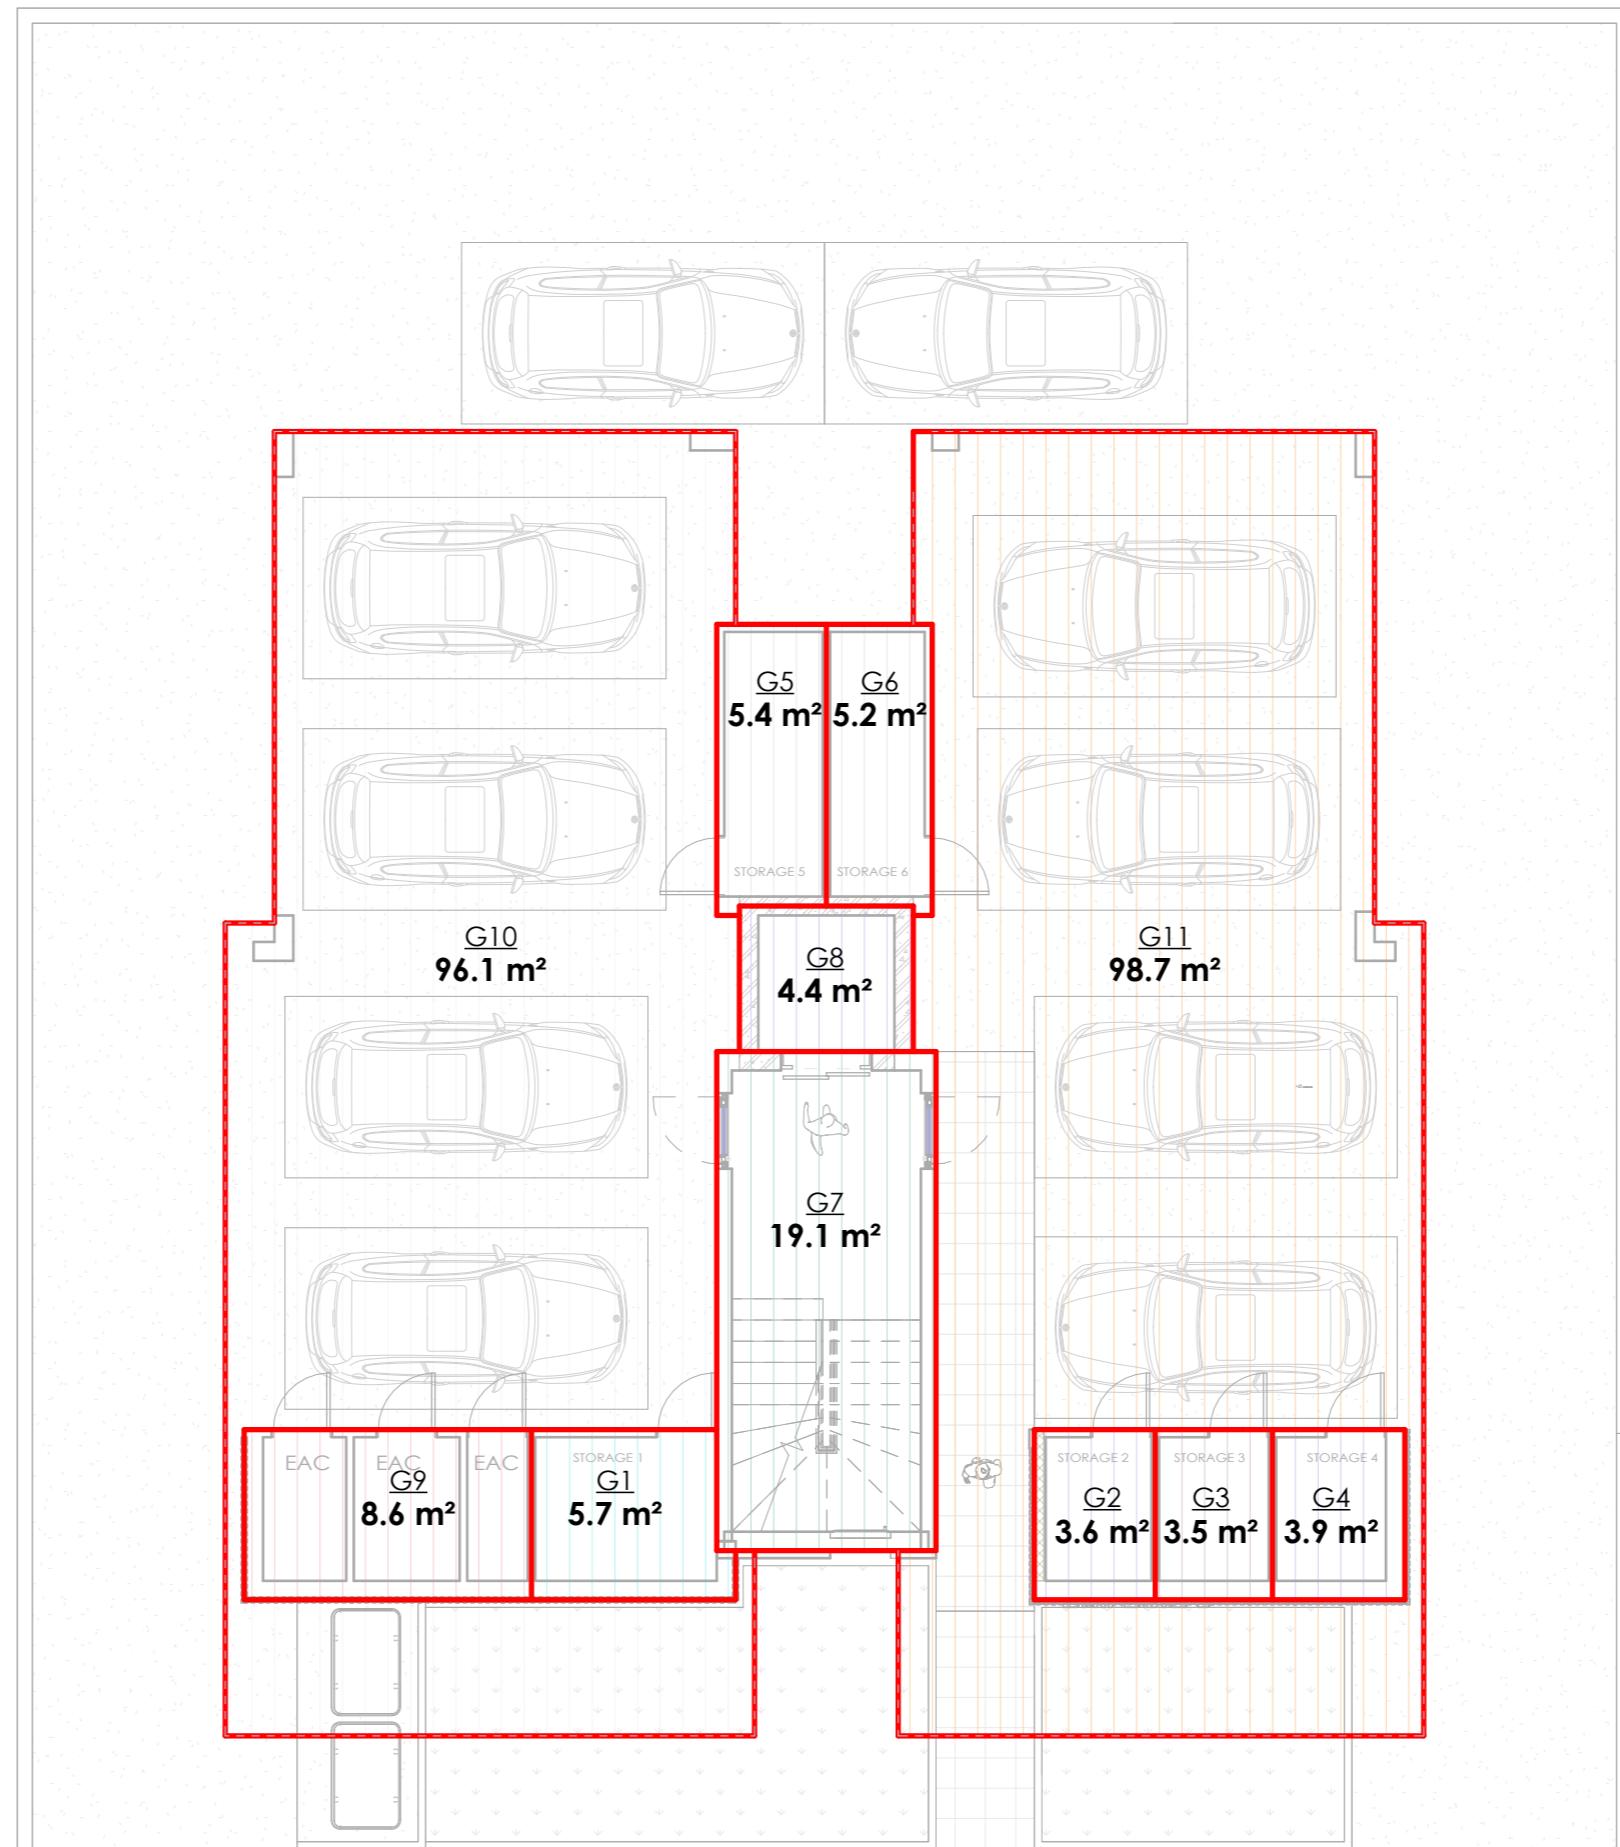

**GROUND FLOOR AREA PLAN**

1 : 100

E1




Phones	Fax
+357 99 882907	+357 24 650846
+357 99 640508	

<b>Address</b>
Nikodimou Milona 28, Sunorama House, off. 401, 6050 Larnaka

<b>Email:</b>
<a href="mailto:info@cgchristou.com">info@cgchristou.com</a>

<b>Description</b>
--------------------

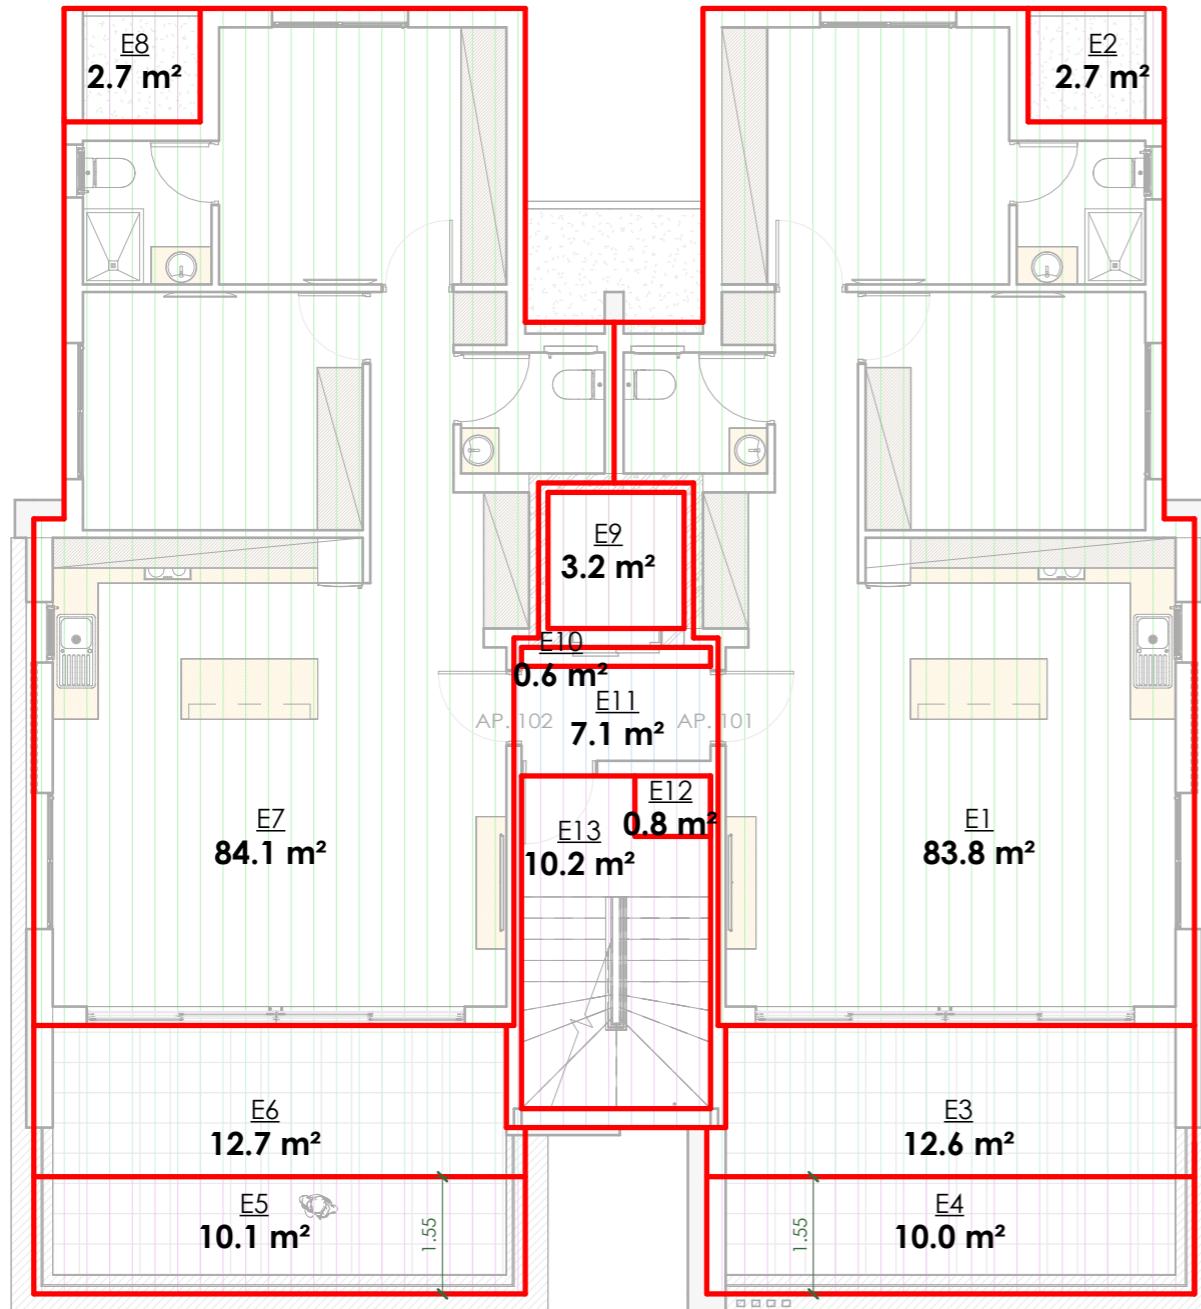

Εμβαδόν ΟΙΚΟΠΕΔΟΥ σύμφωνα με τον τίτλο = 521 m<sup>2</sup>

Ζώνη Κα5 , Οικιστική Ανάπτυξη

Επιτρεπόμενη κάλυψη = 521 X 50% = 260.5 m<sup>2</sup>

Επιτρεπόμενη δόμηση = 521 X 100% = 521 m<sup>2</sup>

Επιπλέον Δόμηση λόγω φωτοβολταικών : 521 X 100% X 5% = 26.05 m<sup>2</sup>

Σύνολο Επιτρεπόμενης δόμησης : 521 + 26.05 = 547.05 m<sup>2</sup>

ΔΟΜΗΣΗ= ( E1+E7+E11 ) X 3 + E13 X 2 = 545.4 m<sup>2</sup> (104.6 %)

ΚΑΛΥΨΗ= E1+E2+E3+E6+E7+E8+E9+E10+E11+E12+E13= 220.5 m<sup>2</sup> (42.32 %)

<b>Client Name</b>
PAPANTONIS NIKOLAIDIS

<b>City/Village</b>
LIMASSOL / ZAKAKI

<b>Sheet Name</b>
FIRST FLOOR AREA PLAN

<b>Project number</b>
09/23

<b>Date</b>
Sheet number

<b>Sheet number</b>
E2

<b>Scale</b>
1 : 100

## FIRST FLOOR AREA PLAN

1 : 100




Phones	Fax
+357 99 882907	+357 24 650846
+357 99 640508	

**Address**  
Nikodimou Milona 28,  
Sunorama House, off. 401,  
6050 Larnaka

**Email:**  
[info@cgpchristou.com](mailto:info@cgpchristou.com)

**Description**

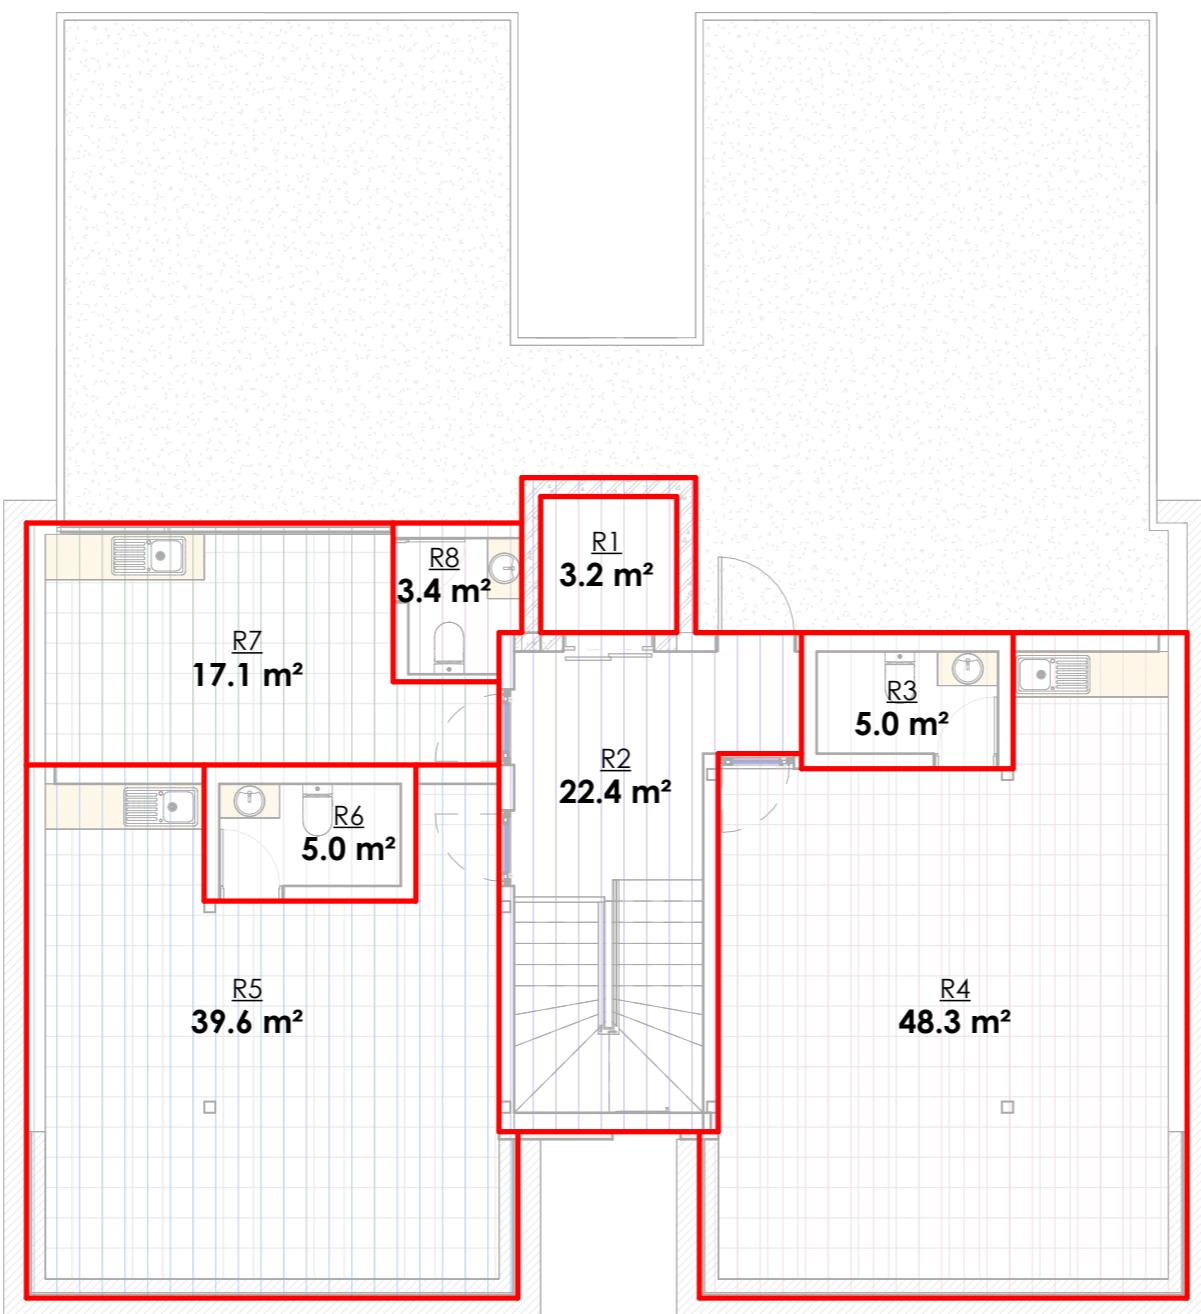

**GARDEN ROOF FLOOR AREA PLAN**

1 : 100

**Client Name**  
PAPANTONIS NIKOLAIDIS

**City/Village**  
LIMASSOL / ZAKAKI

**Sheet Name**  
GARDEN ROOF AREA  
PLAN

**Project number**

**Date** 09/23

**Sheet number**

E3

**Scale** 1 : 100